
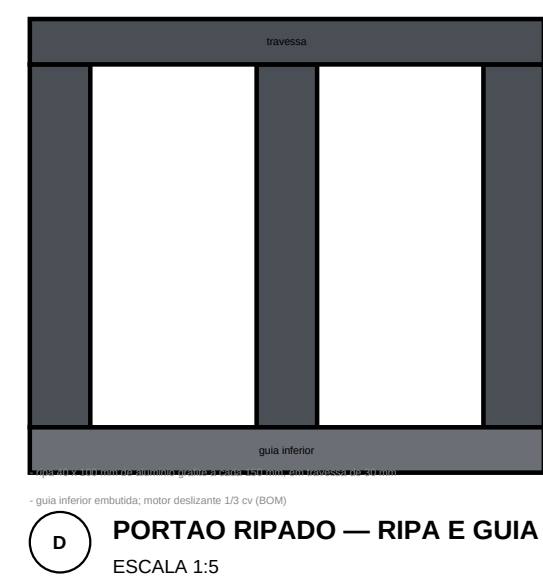
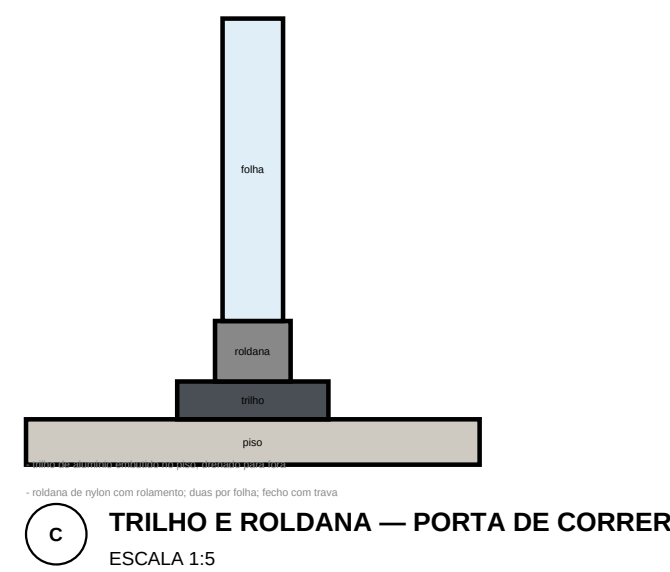
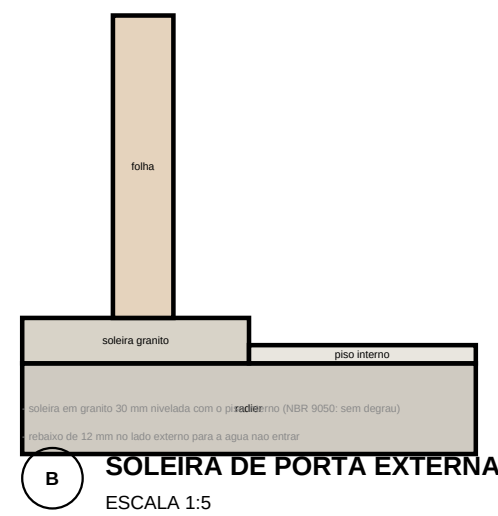


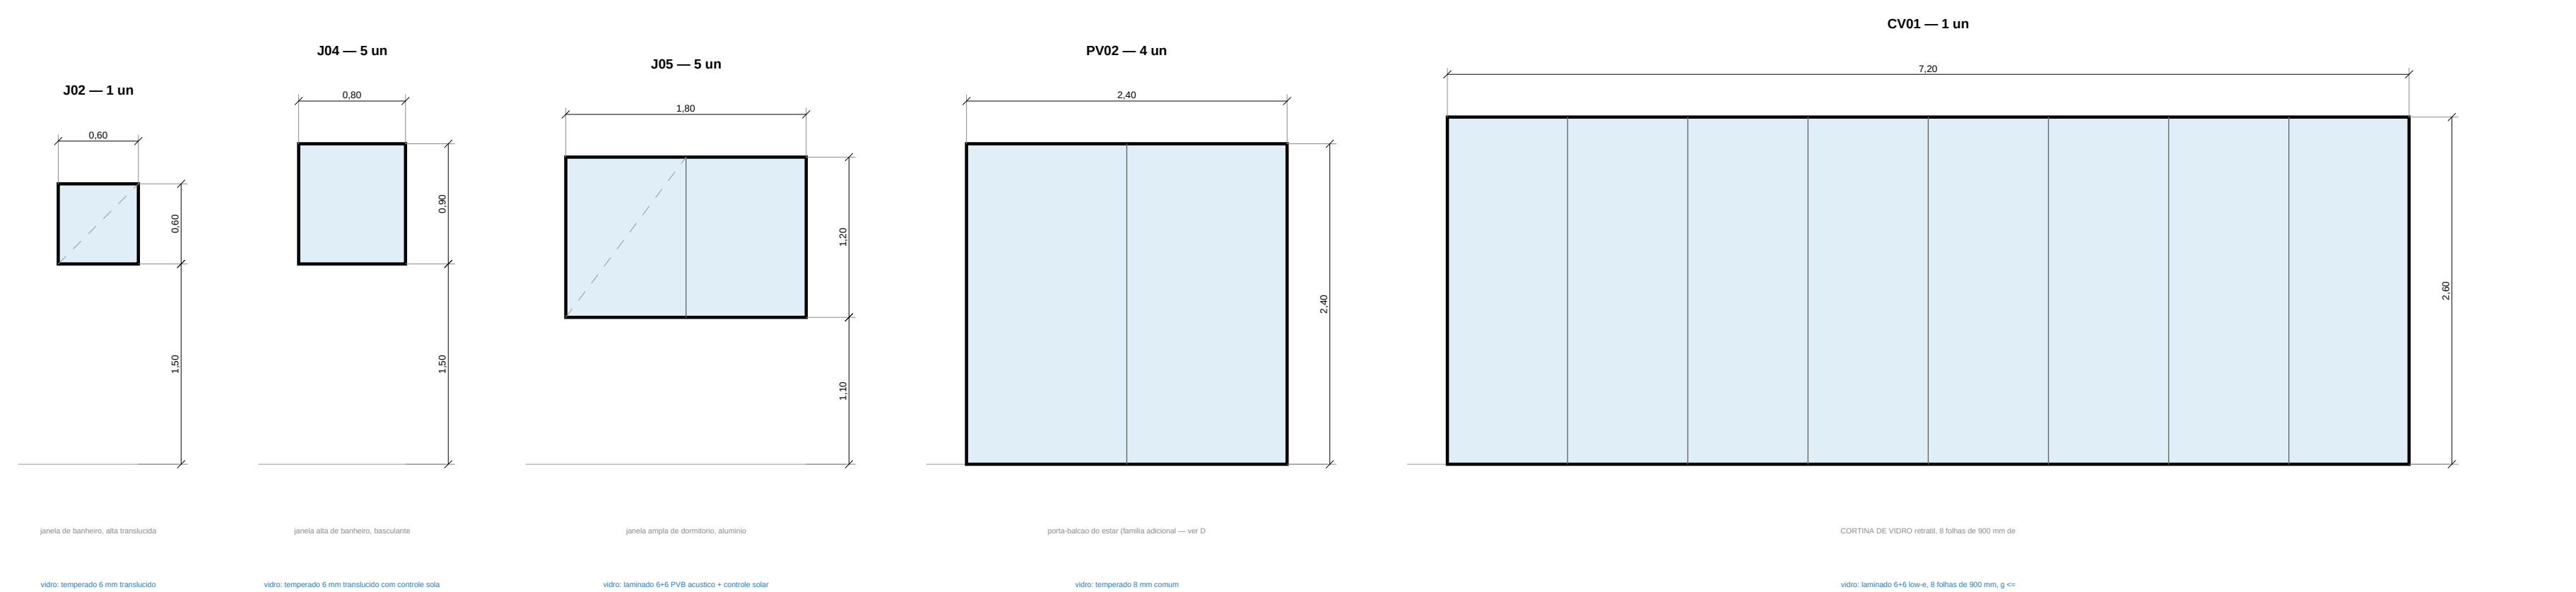

PROJETO PORTO REAL			
RESIDENCIA UNIFAMILIAR MANAUS - AM 10/25 JULIANA PIS			
PROJETO ARQUITETONICO			
ESQUADRIAS — TIPOS, QUANTIDADES E DETALHES			
BASE GEOMETRICA Lista Consolidada pro-022 (previsto) LEGENDA MESTRE: 001	ESCALA 1:40 • 1:5 FORMATO A1 MANAUS 000/000/000	ENVIADO ESTUDO PRELIMINAR R12 VIAO LEROUCK PARA OBRA SEN AMT / RMT	PRONTO 52 ON 78 REV REZ