



1 ISOMETRICO DE ESGOTO E VENTILACAO
ESCALA 1:75

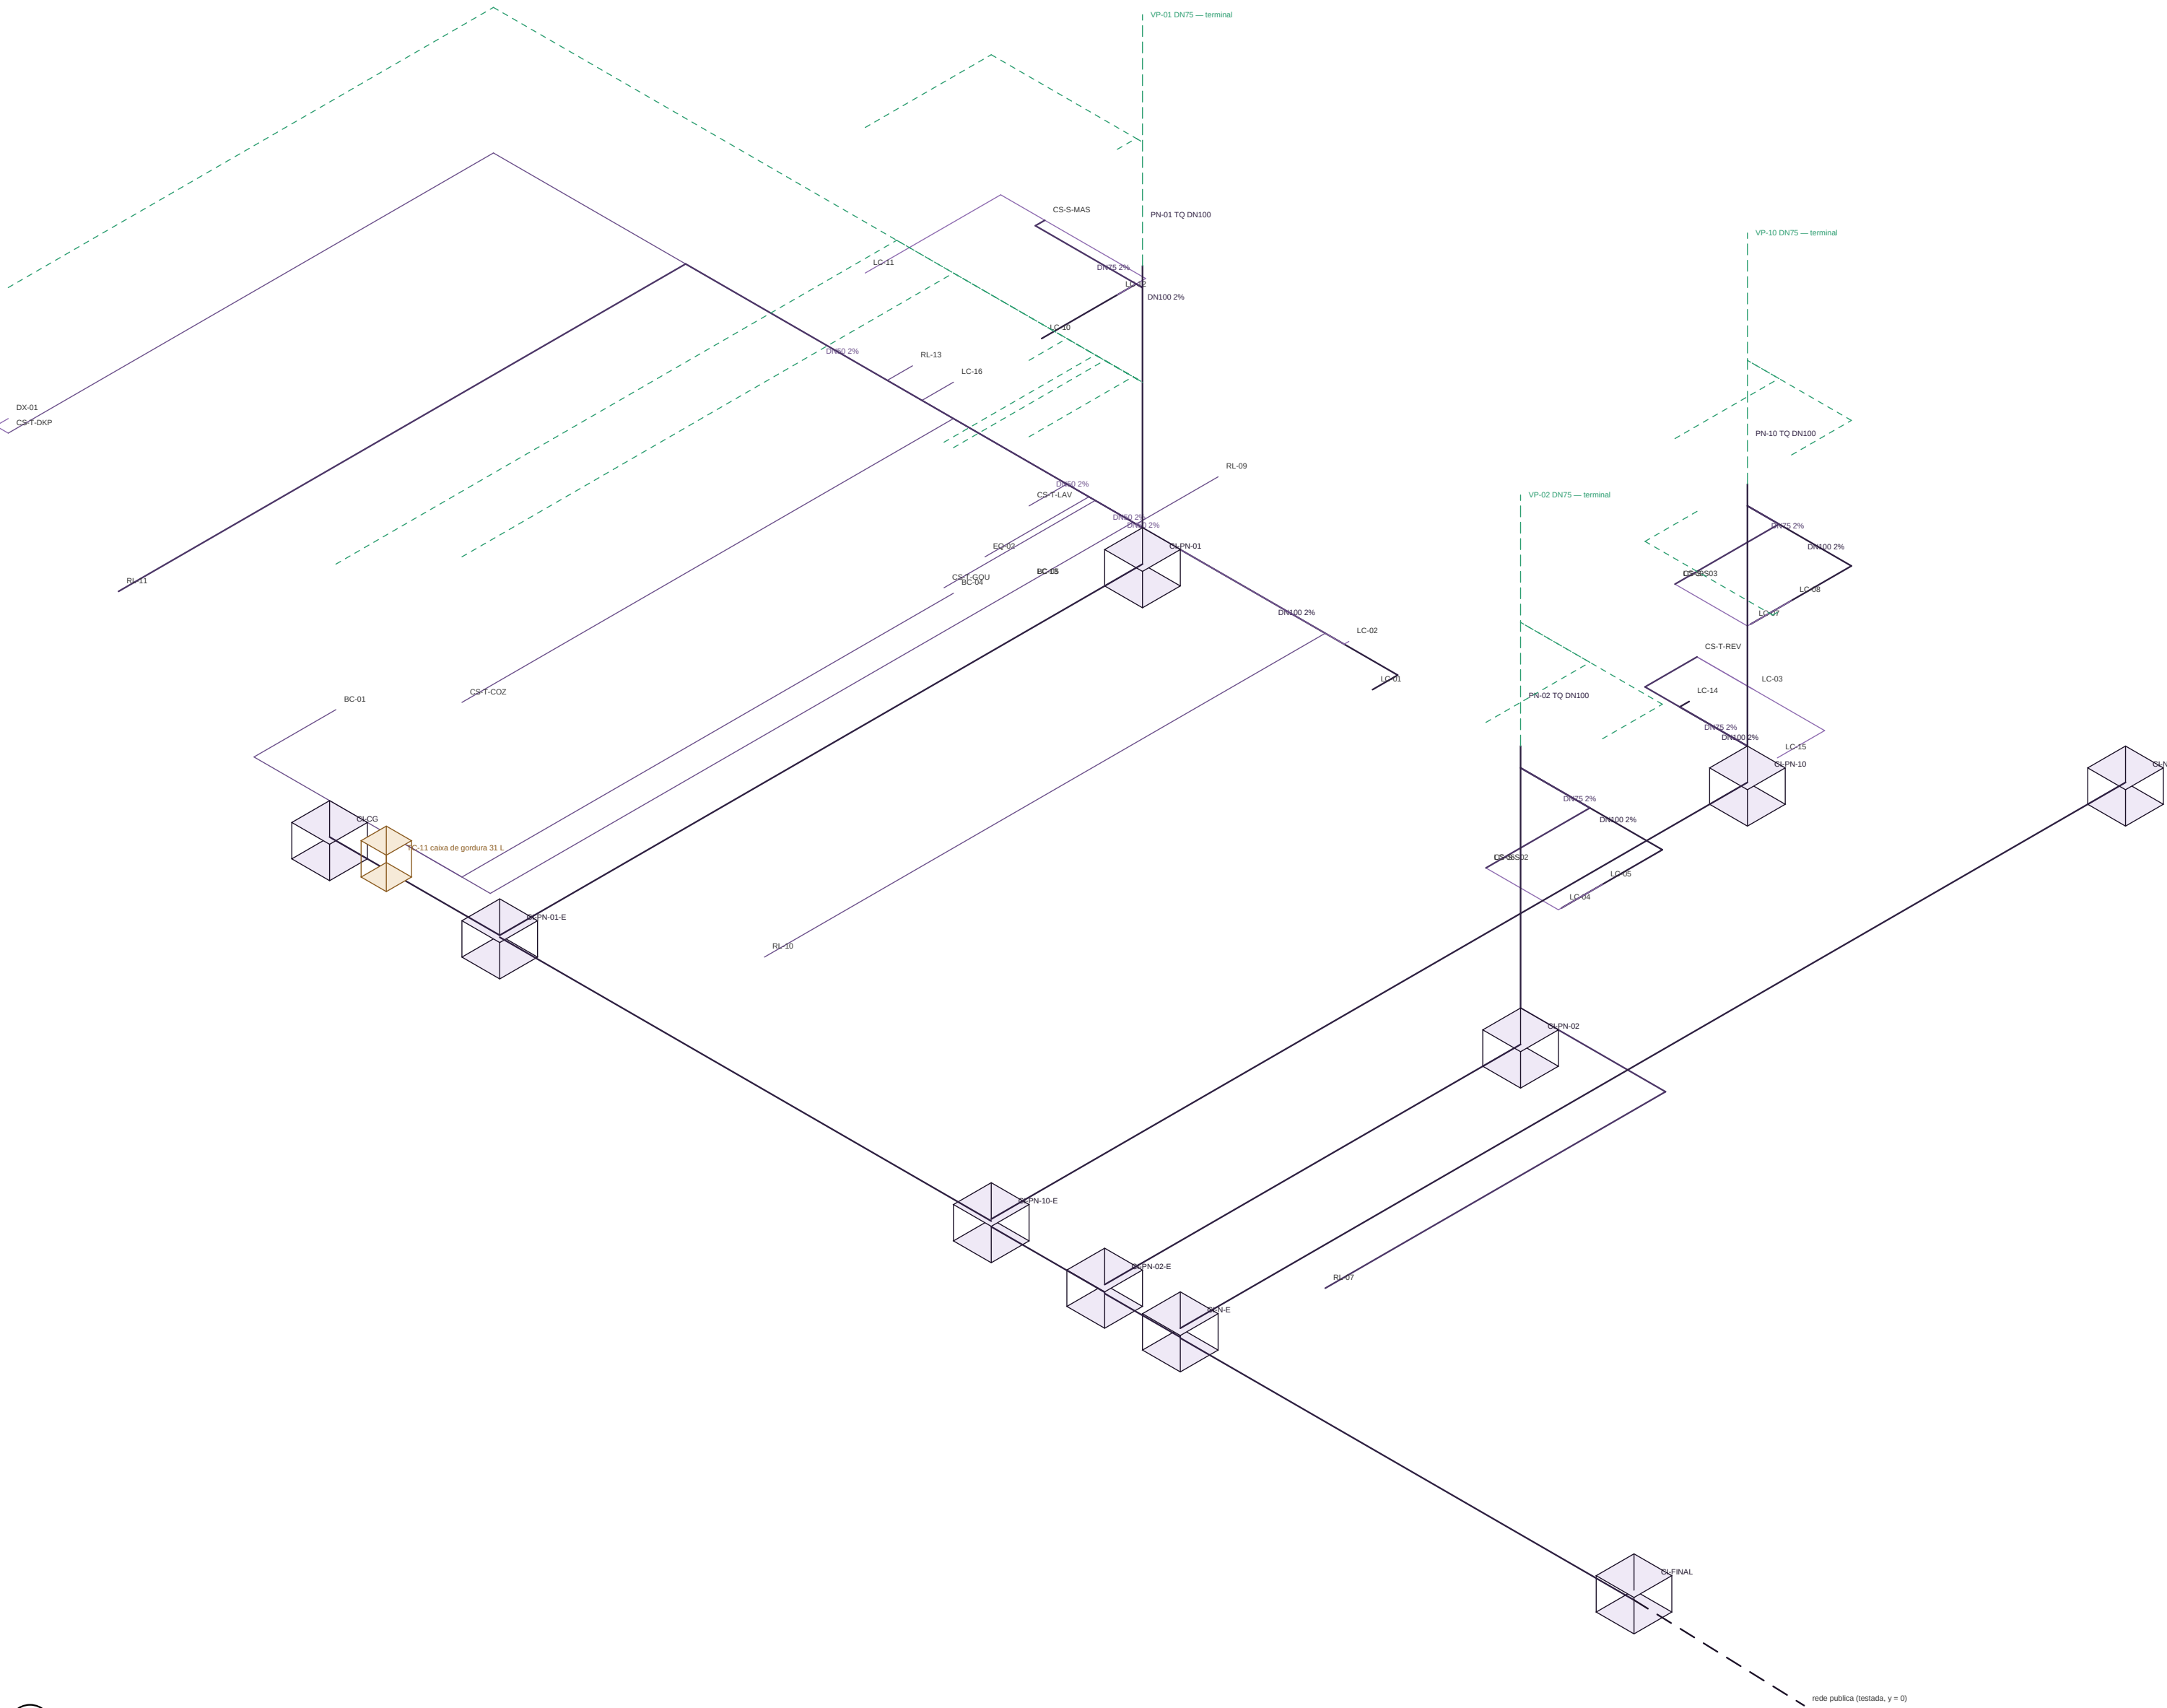

2 PLANTA DE CAIXAS DE INSPECAO E COLETOR
ESCALA 1:150

COLETOR — COTA DE FUNDO (mm, RN = piso do terreno)

DE	PARA	DN	L.m	1	FUNDO MONT.	FUNDO AIS.	PROF. AIS.
CPIN-01	CPIN-02 E	DN200	18,2	2%	—	—	—
CPIN-02	CPIN-02 E	DN200	6,6	2%	—	—	—
CPIN-10	CPIN-02 E	DN200	12,0	2%	—	—	—
CH-E	CH-E	DN200	15,0	2%	—	—	—
CH-02	CPIN-02 E	DN200	2,7	1%	405	427	588
CPIN-02 E	CPIN-02 E	DN200	7,9	1%	307	405	527
CPIN-02 E	CPIN-02 E	DN200	1,8	1%	405	423	435
CH-E	CH-E	DN200	1,2	1%	423	435	423
CH-E	CH-FINAL	DN200	7,2	1%	405	397	435

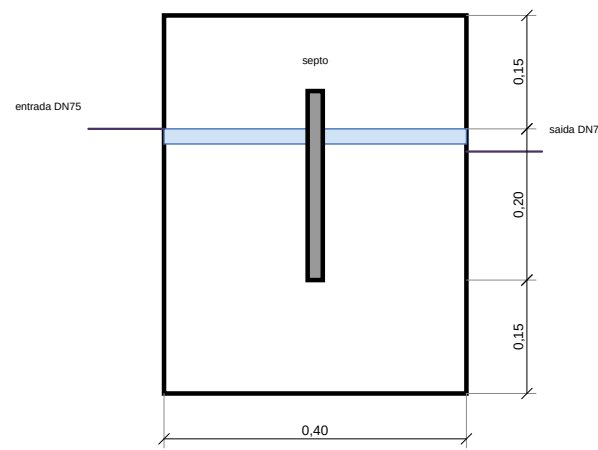

3 CAIXA DE GORDURA 31 L — hermetica, inspecionavel
ESCALA 1:10

RAMAIS — 34

PEÇA	AMB	TIPO	DN	URC	1	L.m	DESTINO	VENT.
LC-01	T-02P	vento	DN200	6	2%	6,6	CPIN-01	sem
LC-02	T-02P	ventoso	DN200	1	2%	2,2	CPIN-01	sem
LC-03	T-REV	box	DN200	2	2%	1,1	CS-T-REV	sem
LC-14	T-REV	vento	DN200	6	2%	1,5	CPIN-10	sem
LC-15	T-REV	ventoso	DN200	1	2%	3,3	CS-T-REV	sem
LC-04	S-REV	vento	DN200	6	2%	4,4	PM-02	sem
LC-05	S-REV	ventoso	DN200	1	2%	2,2	CS-S-REV	sem
LC-06	S-REV	box	DN200	2	2%	0,9	CS-S-REV	sem
LC-07	S-REV	vento	DN200	6	2%	3,9	PM-10	sem
LC-08	S-REV	ventoso	DN200	1	2%	2,2	CS-S-REV	sem
LC-09	S-REV	box	DN200	2	2%	0,9	CS-S-REV	sem
LC-10	S-REV	vento	DN200	6	2%	3,9	PM-01	sem
LC-11	S-REV	ventoso	DN200	1	2%	3,4	CS-S-REV	sem
LC-12	S-REV	box	DN200	2	2%	2,5	CS-S-REV	sem
LC-13	T-LAV	sanita	DN200	3	2%	2,2	CPIN-01	sem
LC-16	T-LAV	sanita	DN200	3	2%	4,4	CPIN-03	sem
LC-17	T-02P	sem	DN200	3	2%	4,4	TC-11	sem
BC-04	T-02P	sem	DN200	3	2%	10,8	TC-11	sem
BC-05	T-LAV	sem	DN200	3	2%	12,2	TC-11	sem
BC-06	T-LAV	sanita	DN200	3	2%	3,0	CPIN-01	sem
BC-01	T-02P	sanita	DN200	2	2%	0,9	CS-T-02P	sem
CS-T-REV	T-REV	caixa sif.	DN200	4	2%	2,9	CPIN-10	sem
CS-S-REV	S-REV	caixa sif.	DN200	4	2%	3,3	PM-02	sem
CS-S-REV	S-REV	caixa sif.	DN200	4	2%	2,6	PM-10	sem
CS-S-REV	S-REV	caixa sif.	DN200	4	2%	2,2	PM-01	sem
CS-T-LAV	T-LAV	caixa sif.	DN200	1	2%	2,2	CPIN-01	sem
CS-T-02P	T-02P	caixa sif.	DN200	1	2%	15,0	CPIN-01	sem
CS-T-02P	T-02P	caixa sif.	DN200	3	2%	15,4	CPIN-01	sem
CS-T-02P	T-02P	caixa sif.	DN200	1	2%	3,8	CPIN-01	sem
RL-13	T-02P	sem	DN200	1	2%	5,3	CPIN-01	sem
RL-07	T-02P	sem	DN200	1	2%	9,2	CPIN-02	sem
RL-11	T-LAV	sem	DN200	1	2%	15,5	CPIN-01	sem
RL-08	T-VRL	sem	DN200	1	2%	1,7	CPIN-01	sem
RL-10	T-LAV	sem	DN200	1	2%	14,2	CPIN-01	sem

NOTAS

- 1. Ramal de descarga por peça com DN da NBR 5200; comprimento 2% em toda a rede predial (a norma permite 1% em DN100) — a decisão "sem nos entupir" — coleta enterrada a 1%.
- 2. Lavatório, box e vaso de cada banheiro caem em caixa sifonada 200 x 150 x 150 mm, vaso direto ao tubo de queda ou a caixa de inspeção. 15 ramais de ventilação DN200 onde a altura fica além da distância da tabela 5.
- 3. 17 caixas de inspeção 900 x 600 que de cada tubo de queda, frente, encanimento de 20 x 10. Fundo final a 0,75 m no total, no sentido em que o tubo desce (PFO) — a profundidade não cresce.
- 4. Caixa de gordura CGD — caixa de gordura sempre de 31 L a partir de dois pontos, tubos de queda DN100 com terminal de ventilação 300 mm acima da cobertura.

PROJETO PORTO REAL

RESIDENCIA UNIFAMILIAR (MANSÃO - AM) | SOBR TATIANA-PS

PROJETO ARQUITETONICO

ESGOTO SANITARIO E VENTILACAO — ISOMETRICO, CAIXAS E COLETOR

BASE GEOMETRICA	ESCALA	EXIBICAO	PRINCIPA
União Consolidada	1:75 · 1:150 · 1:10	ESTUDO PRELIMINAR R2	62
Projeto (previsão)	FORMATO A1	NAO LIBERADO PARA OBRA	62
UNIDADE MEDIDA: mm	UNIDADE MEDIDA: mm	SEM ART / INT	62