




1 CORTE LONGITUDINAL (SUL -> NORTE)
ESCALA 1:25

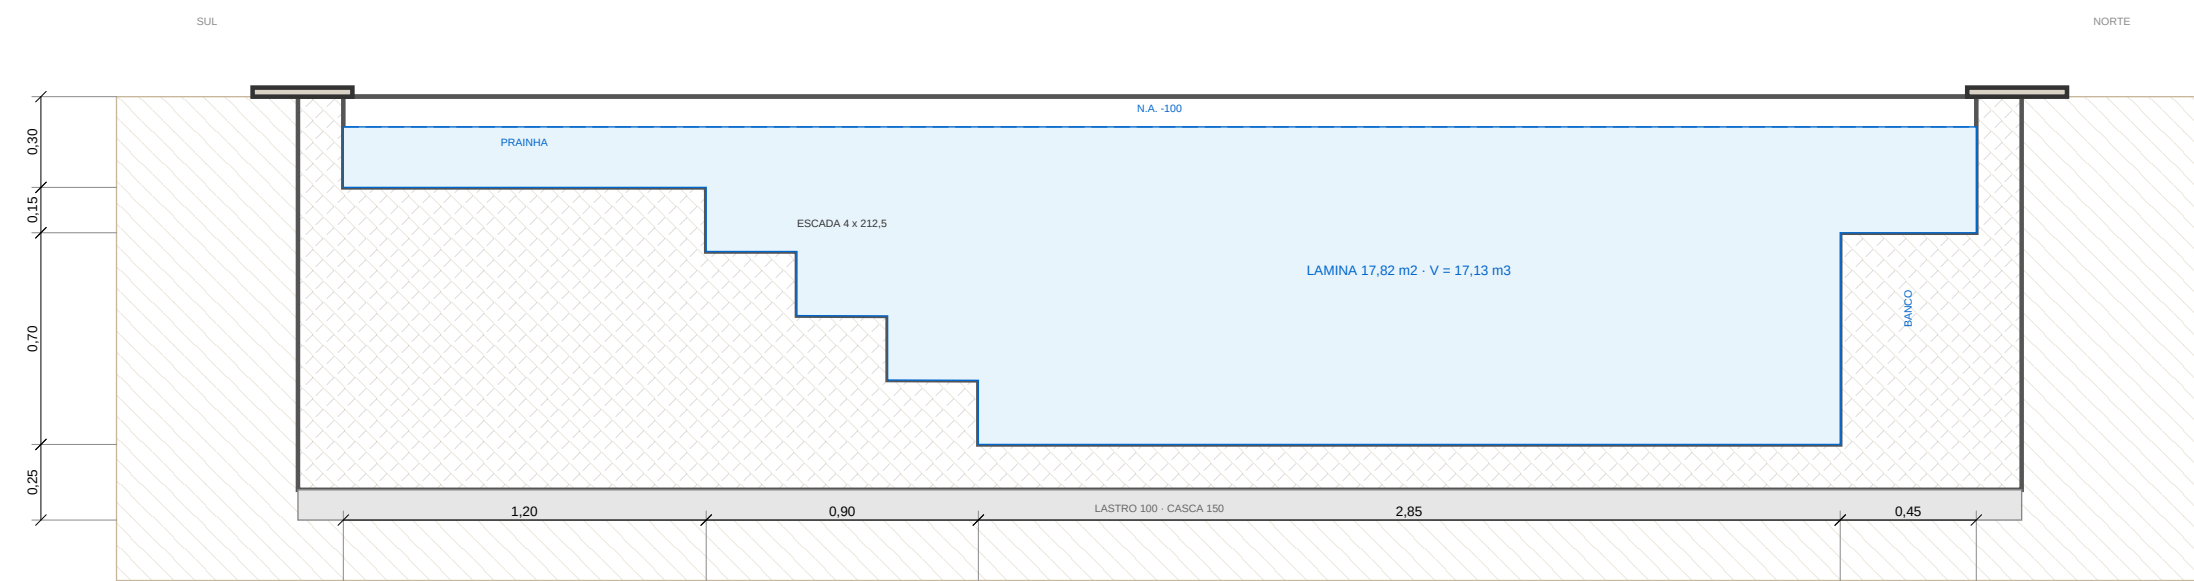


2 CORTE TRANSVERSAL PELO DRENO (LESTE -> OESTE)
ESCALA 1:25

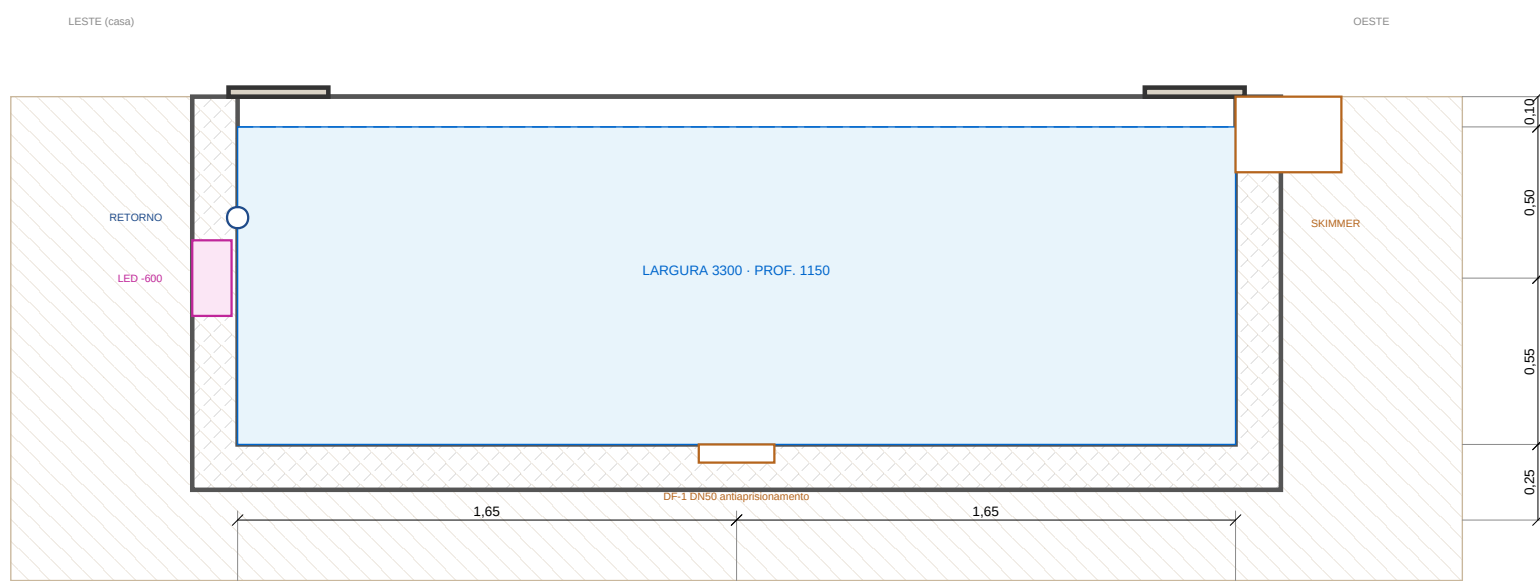


3 ESCADA DE PRAIA
ESCALA 1:10

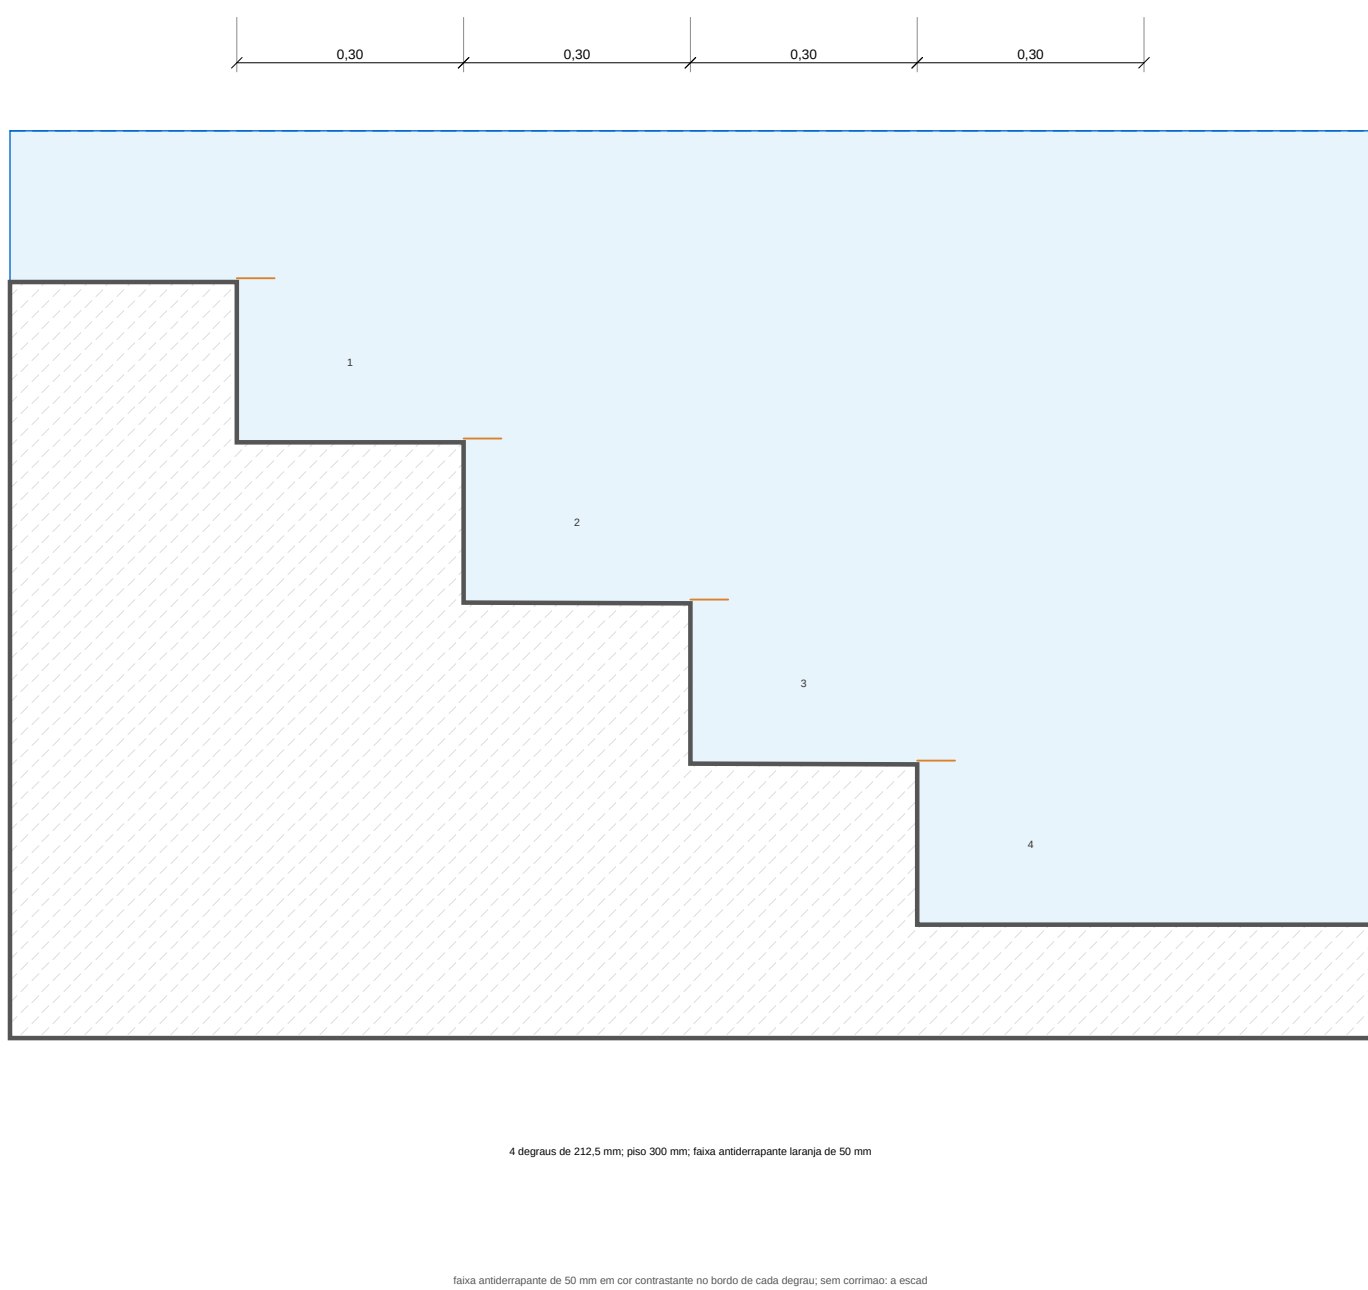


4 BORDA COM PINGADEIRA E FAIXA SECA
ESCALA 1:5

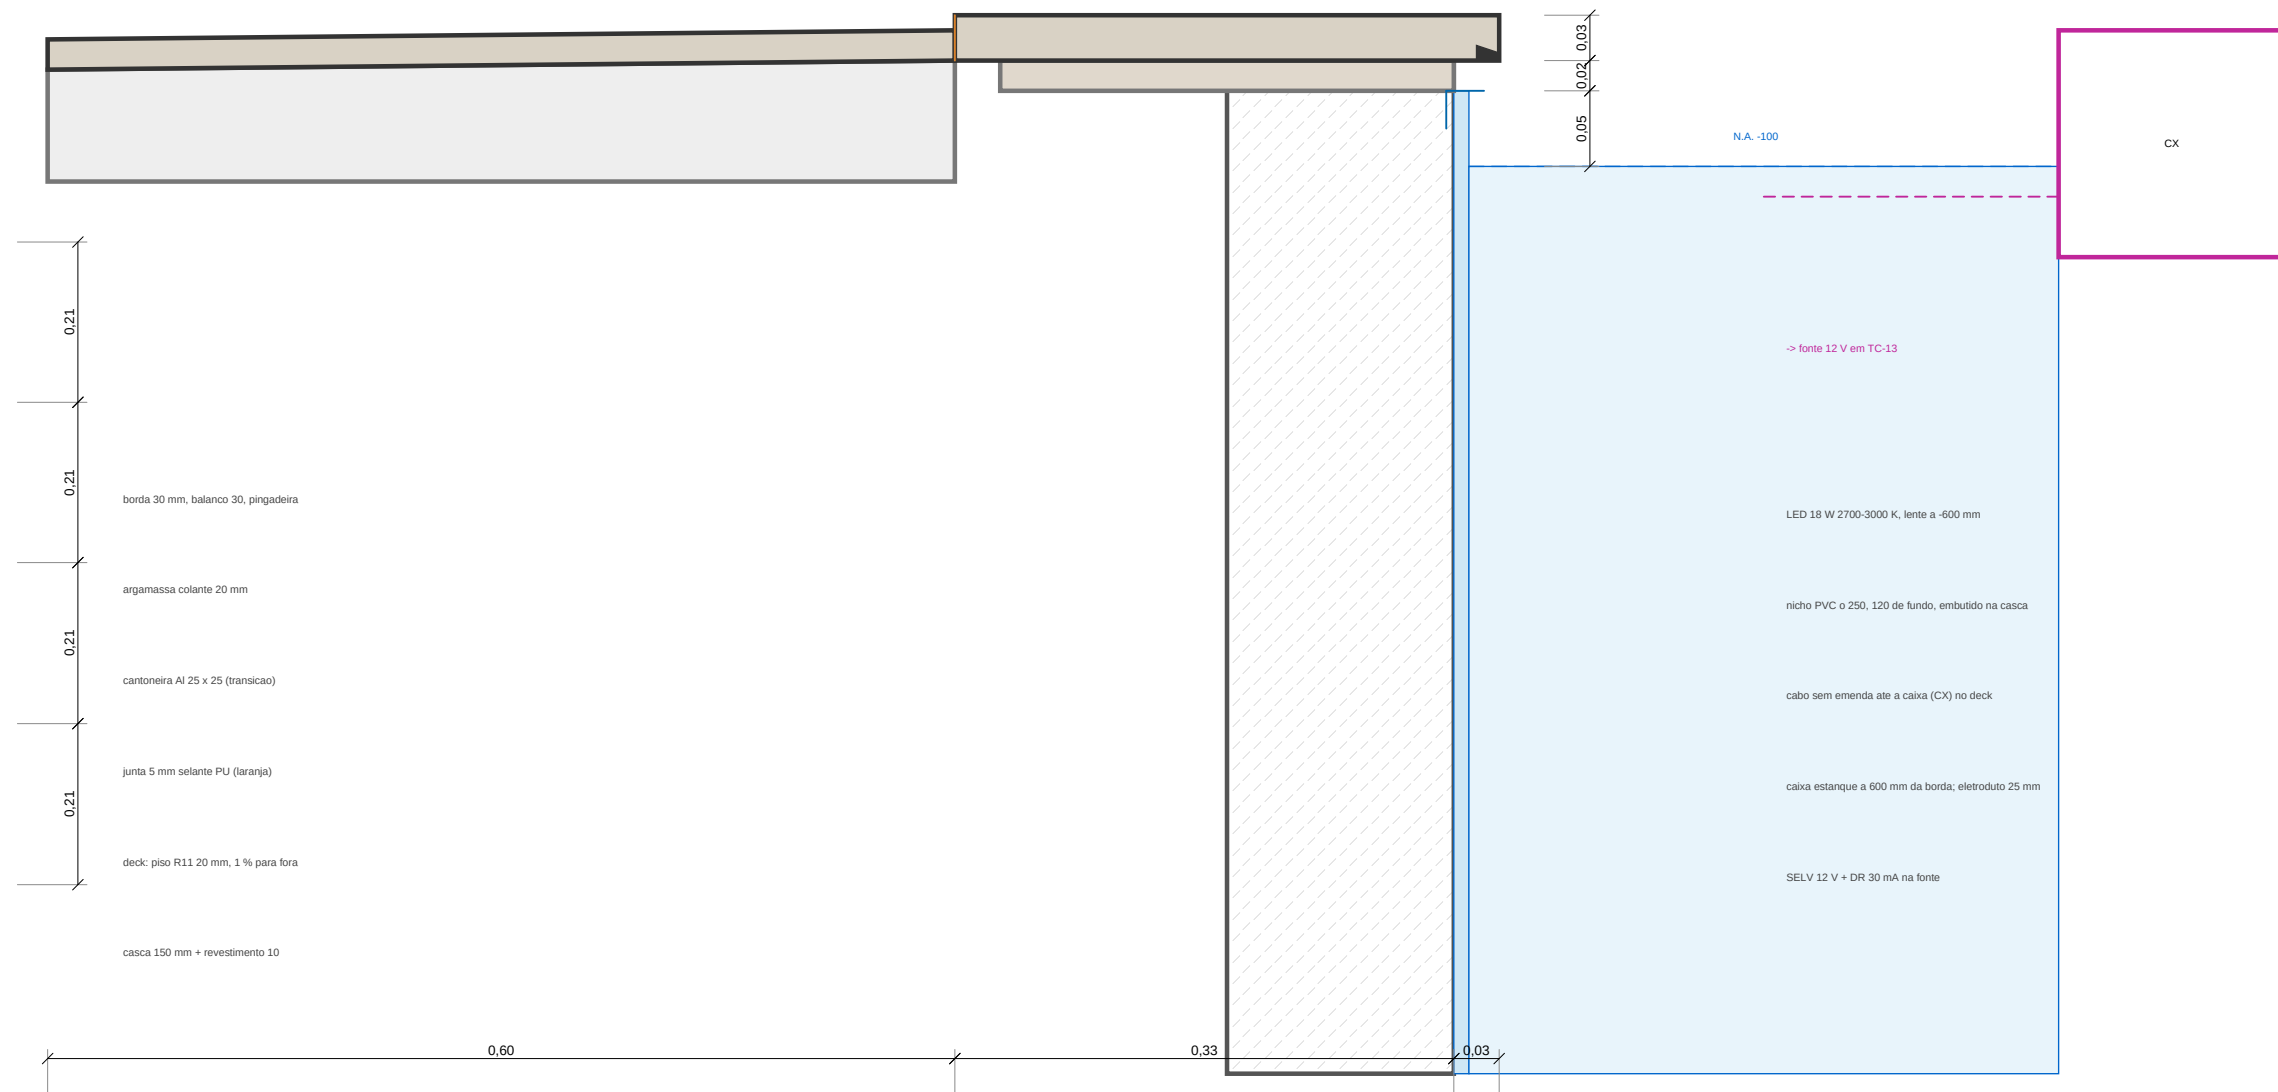

5 NICHOS DO LED E CAIXA DE PASSAGEM
ESCALA 1:5

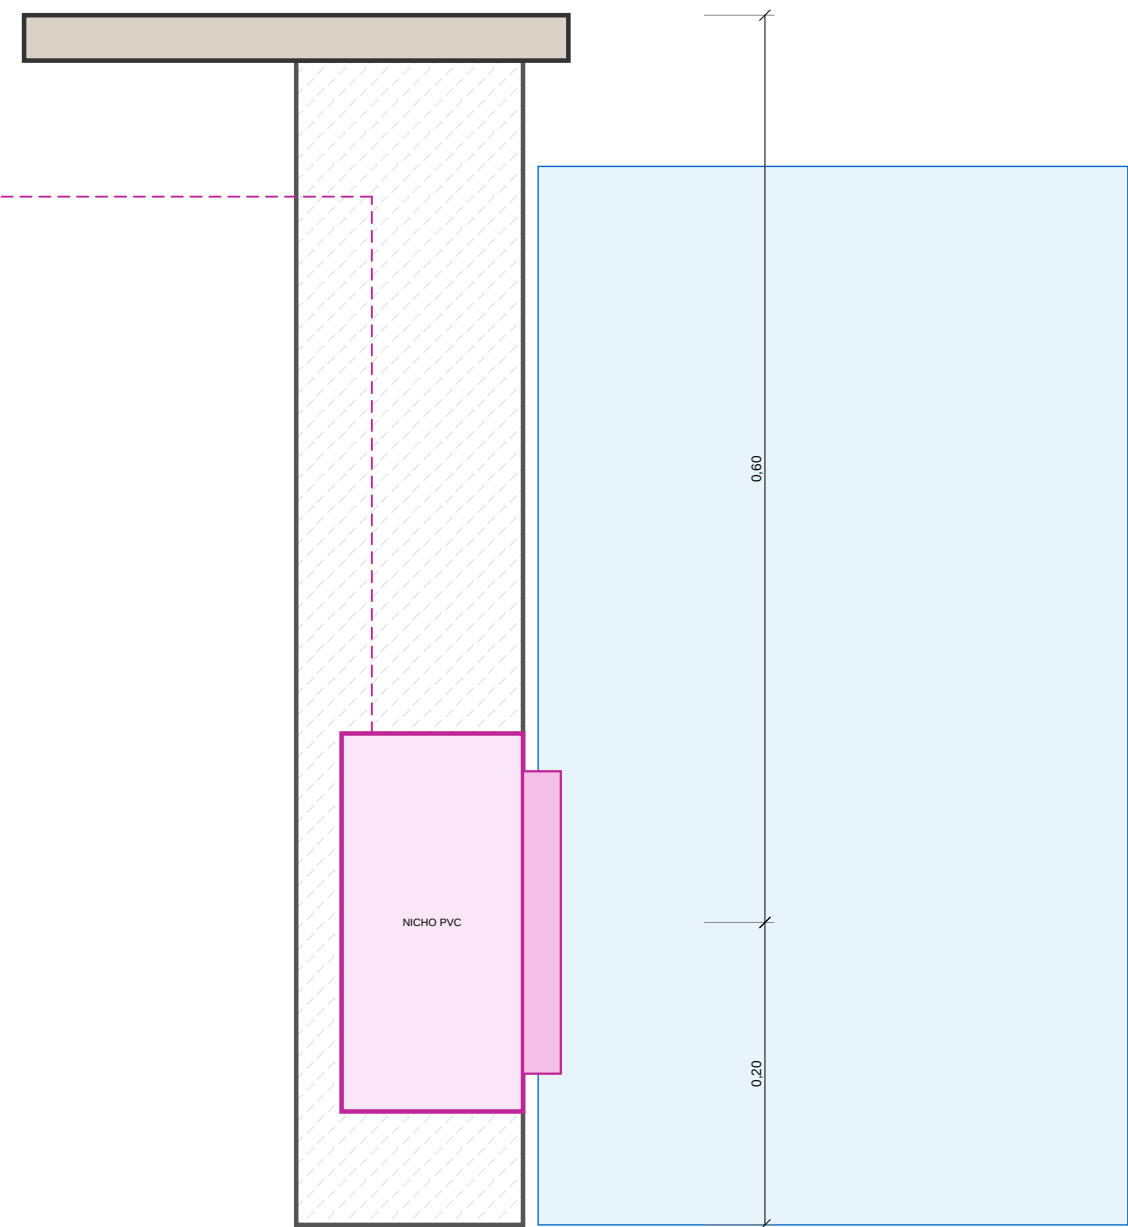

6 PLANTA DE ILUMINACAO SUBAQUATICA
ESCALA 1:50

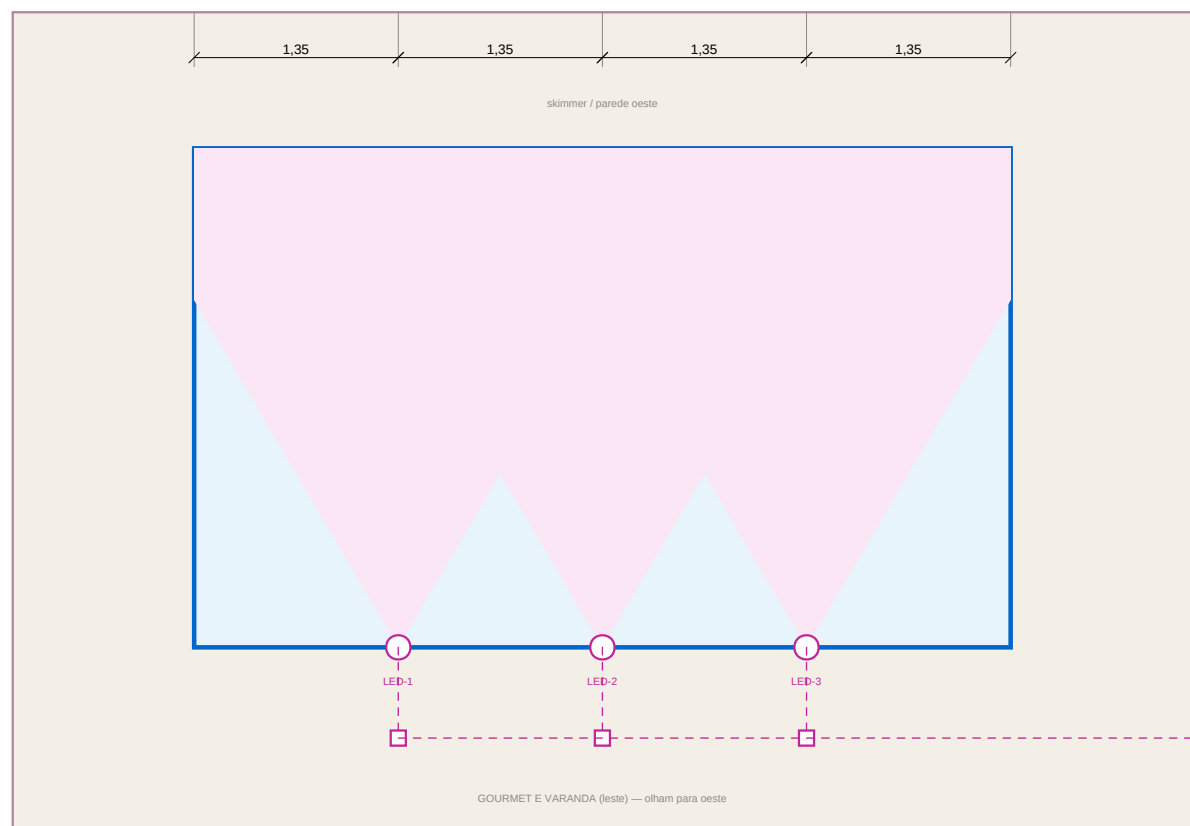

ITEM	VALOR	COMENTÁRIOS
Letreiro volume	17,62 m ² / 17,25 m ²	PRECISA
Nível da água	-10 mm	desnível 10
Plancha	1200 x 300 mm	PRECISA
Escala	4 x 112,5 / 300 mm, altura 800	desnível / 260-90
Fundo	1150 mm planilha 3000	PRECISA
Banca	460 mm, assento x 450	PRECISA
Caixa / leito	160 / 120 mm, encaixado x 1400	desnecessária (9)
Concreto	4,57 m ³	concreto armado 35 MPa, 100%
Impermeabilização	30,43 m ²	area revestida
Força	33 peças de 800 mm; 17,4 m	permetro da lâmina

LED	x mm	z mm	W	len	CABO m	mm2	QUEDA
LED-1	6100	<60	18	1030	12,8	1,5	3,7 %
LED-2	7900	<60	18	1030	11,5	1,5	3,3 %
LED-3	8950	<60	18	1030	10,2	1,5	2,9 %
TOTAL			54				3,03 Whm2

REGRAS DA ILUMINACAO

REGRA	PROJETO
Lado	gerado livre: a mais perto do gourmet, que fica para oeste – a largada
Fora	fonte SELV 12 V, 70 VA, no quarto entreposto de TC-13, protegida por GDI
Nicho	nicho do PVC embutido na casca, com calças de passageiro estacione no deck
Previsão específica	3,03 Win2 na faixa 2.0-4.0 (4)

CONFERENCIAS DESTA PRANCHA

Q	QUE	COMO	
cassete, espelho		4 degraus de 212,5 mm (base 250)	ca
cassete piso		360 mm (para 360)	ca
cassete caixa no trecho fundo		aproxima 900 mm; bancos colocados a 870e mm	ca
faca saca rol		1200 mm (para 900)	ca
faca saca rolo		1500 mm (para 900)	ca
faca saca rolos		1200 mm (para 900)	ca
faca saca rolos		960 mm (para 660)	ca
faca saca desdobrada por lado conf		não 1200/2000, mas 1200/2200; mais 1200/2200; ouca 800	ca
círculo das placas coroa e bomba e		TUE-17 500 Va coroa C75 Va bomba 801 - fôrme das LEDs	ca
potência do luz por m ²		0,01 W/m² (Dica 2 D-0,5)	ca
quinta e 12 V LED-1		2,68 VA em 1,5 mA/m² x 12,8 m	ca
quinta e 12 V LED-2		3,3 VA em 1,5 mA/m² x 11,9 m	ca
quinta e 12 V LED-3		2,8 VA em 1,5 mA/m² x 10,1 m	ca
LEDs na parede colada para a casa		(paralela Diem's)	ca
painelito da borda e o da BOM		17,4 m x 17,4 m	ca

NOTAS

Nível da água: 100 mm (páremes). Piscina 300 mm: escada de praia de 4 degraus (212,5 x 300 mm) na largura interna. Fundo 1150 mm, banco com assento a 450 mm.

• Estrutura: concreto armado 32 MPa, caixa de 150 mm, sola d'água 150 mm U (15), laje 150 mm, fundo da escanoria a 1400 mm. Impermeabilização: cristalização no concreto fresco + argamassa polimérica bicamadas em 2 demãos (pH teste de estanqueidade de 72 h antes do revestimento).

• Bordas: 600 x 300 x 30 mm, porcelanato P11 da faixa seca, bordo dobrado e parafusado, deck com 1" para fora da piscina, luminária: 3 LEDs 2700-3000 K a 500 mm, SELV 12 V, 3,03 W/m.

• Outros materiais (pH teste químicos de pH livre): 100 litros de água de piscina residencial.

PROJETO PORTO REAL

RESIDÊNCIA UNIFAMILIAR | MANAUS - AM | SU16 TARUMA (H)

PROJETO ARQUITETÔNICO

PISCINA: CORTES, ESCADA, BORDA E ILUMINACAO

BASE GEOMETRICA	ESCALA	EMISSAO	PROVA
Lista Consolidada	indicada	ESTUDO PRELIMINAR R\$2	70
pos #32 (previsto)	FORMATO A1	NÃO LIBERADO PARA OBRA	
UNIDADE MESTRE: 444	MALHA 800/800/350	SEM ART / IMPR	de 78 RE