


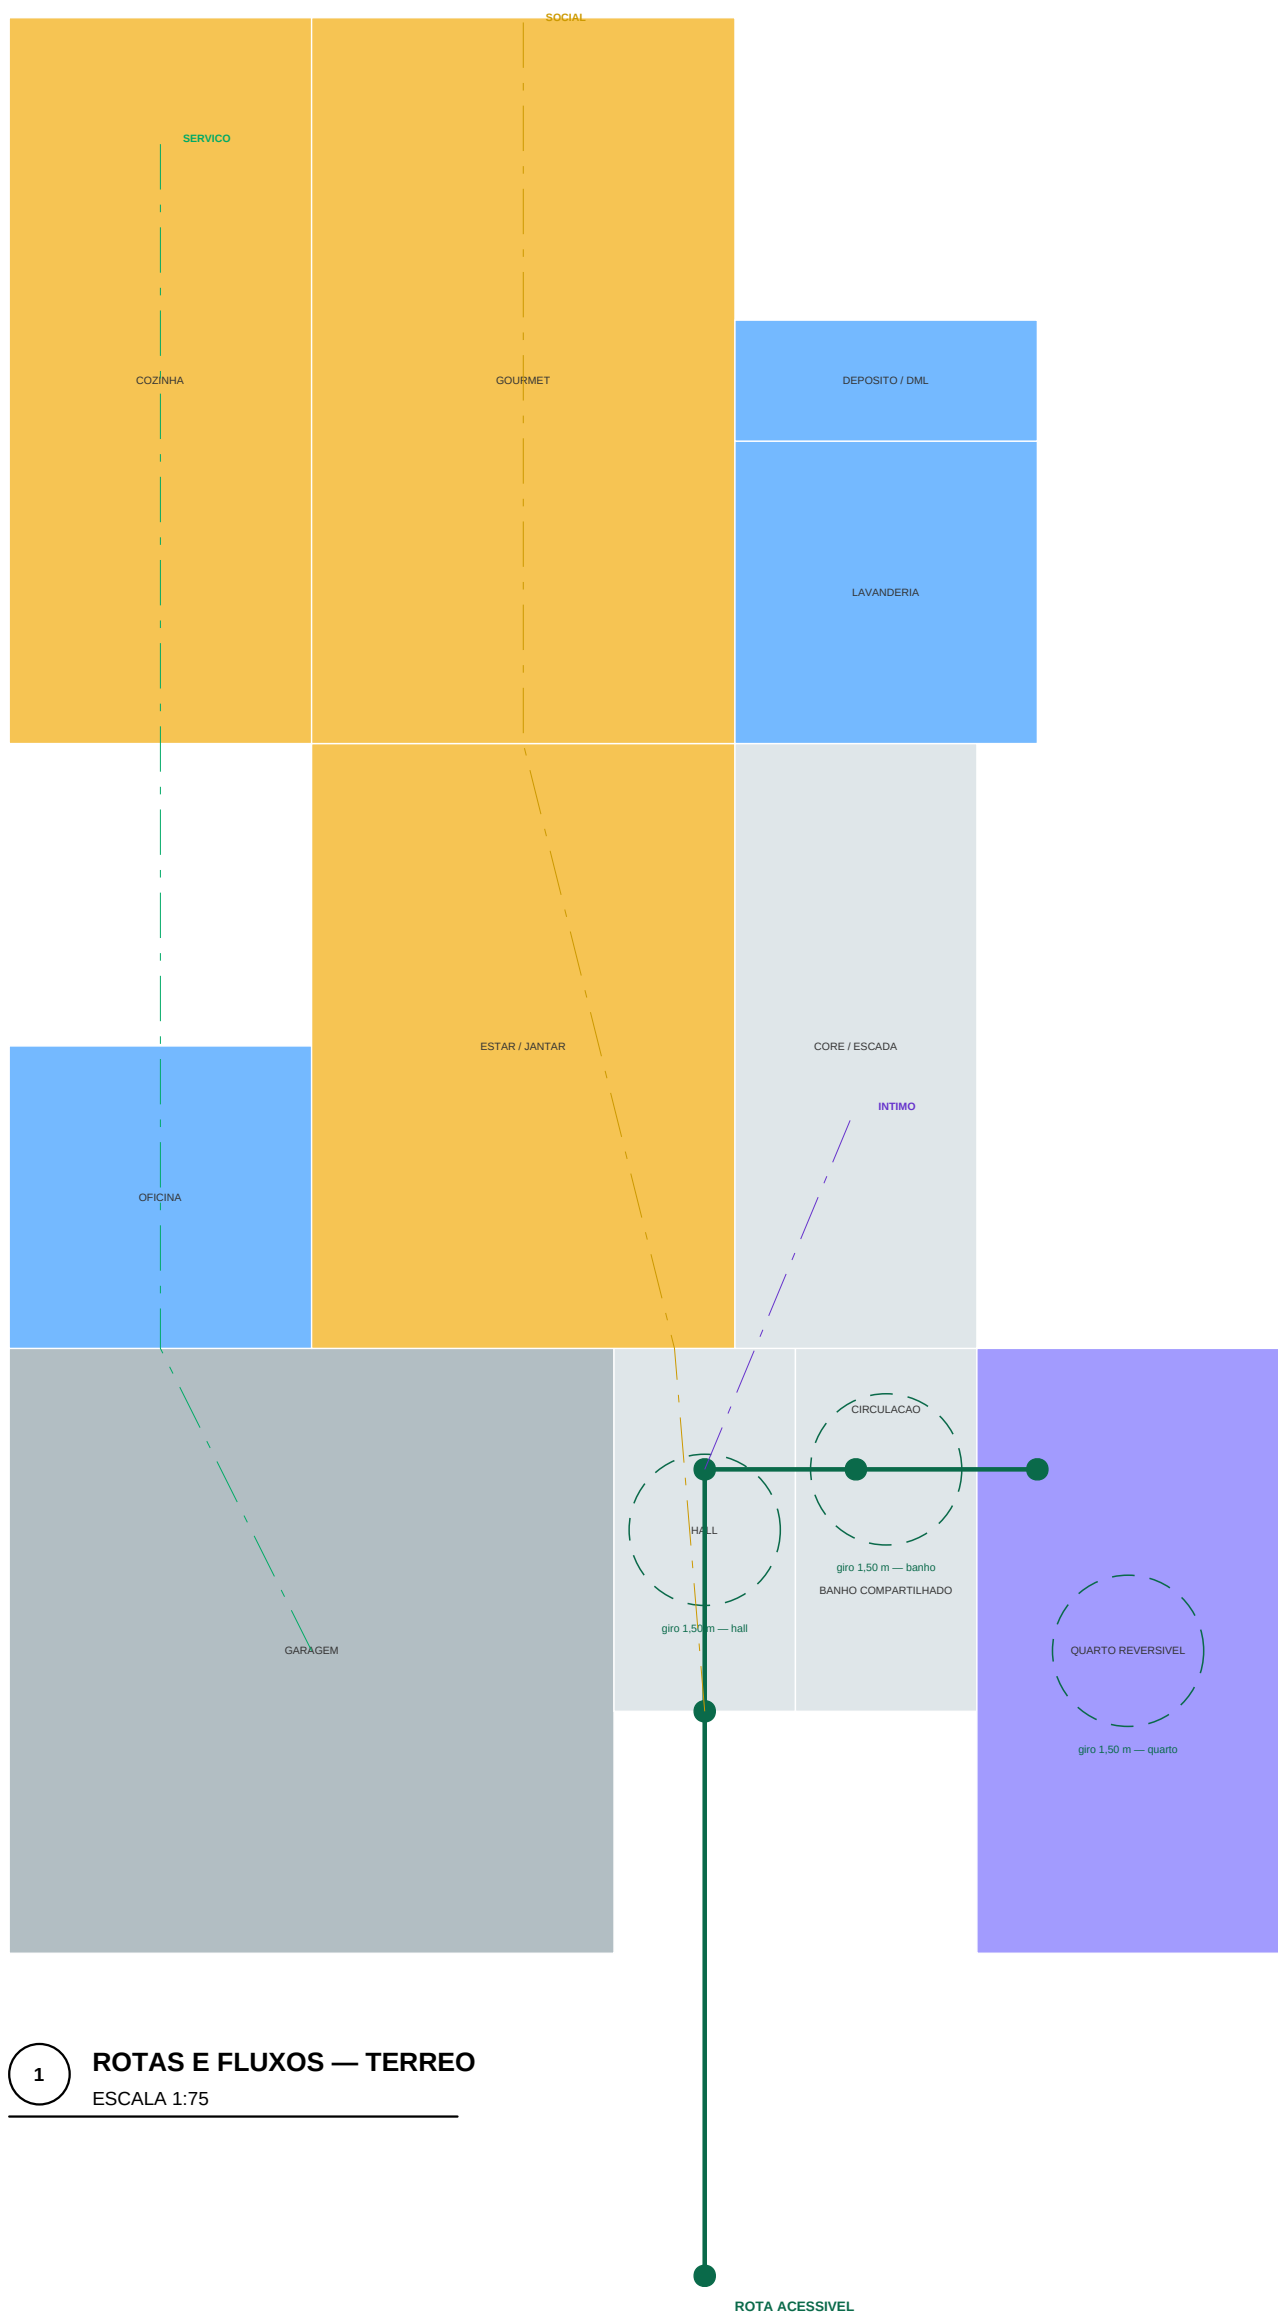


1 ROTAS E FLUXOS — TERREO
ESCALA 1:75

VERIFICACAO NBR 9050

ITEM	EXISTENTE	PROPOSTO	
Vel. livre de porta	800 mm	940 mm (altura de 900)	OK
Circulo de giro 360 graus	1.500 mm	hall, banheiro e quarto	OK
Desnivel sem rampa	até 5 mm	soluções niveladas	OK
Largura de circulação	900 mm	1.800 mm no hall	OK
Barras de apoio	relívios prévios	instaladas na P1 e P10.1	OK
Barrameda acessível	altura livre 750 mm	sem obstáculos até a calha	OK
Corredor e interruptor	600 a 1.000 mm	a definir no eletrico	pendente

FLUXOS — SEPARACAO DE CIRCUITOS

CIRCUITO	PERCURSO	CRIÇA O SOCIAL?
Servico	garagem -> estufa -> lavanderia -> cozinha -> despensa	NÃO
Social	entrada -> hall -> estar -> gourmet -> alameda -> piscina	—
Área íntima	hall -> banheiro compartilhado -> quarto reservável	NÃO
Área íntima	hall -> core -> hall superior -> suíte	NÃO
Área íntima	cozinha -> despensa -> reserv. hall	NÃO

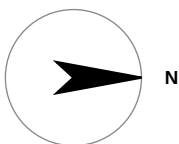

- NOTAS
- * Rota acessível do passeio ao quarto reservável e ao banheiro compartilhado.
 - * Circulo de giro de 1.500 mm verificado nos pontos de manobra.
 - * Porta de correr de 900 mm no banheiro íntima e área de varanda.
 - * Reforço para barras de apoio instaladas antes do fechamento das placas.

PROJETO PORTO REAL

RESIDENCIA UNIFAMILIAR (MANAUS - AM) | SUELE TATIANA-PS

PROJETO ARQUITETONICO

ACESSIBILIDADE E FLUXOS

BASE GEOMETRICA Linha Consolidada ISO 9122 (previsão) UNIDADE: METROS - MM	ESCALA 1:75 FORMATO A1 MILIMETROS (50/100/200)	EMISSAO ESTUDO PRELIMINAR R3B NÃO LIBERADO PARA OBRA SEM ART / RNT	PROVA 17 DE 25 REVIZOES
---	--	---	--------------------------------------