


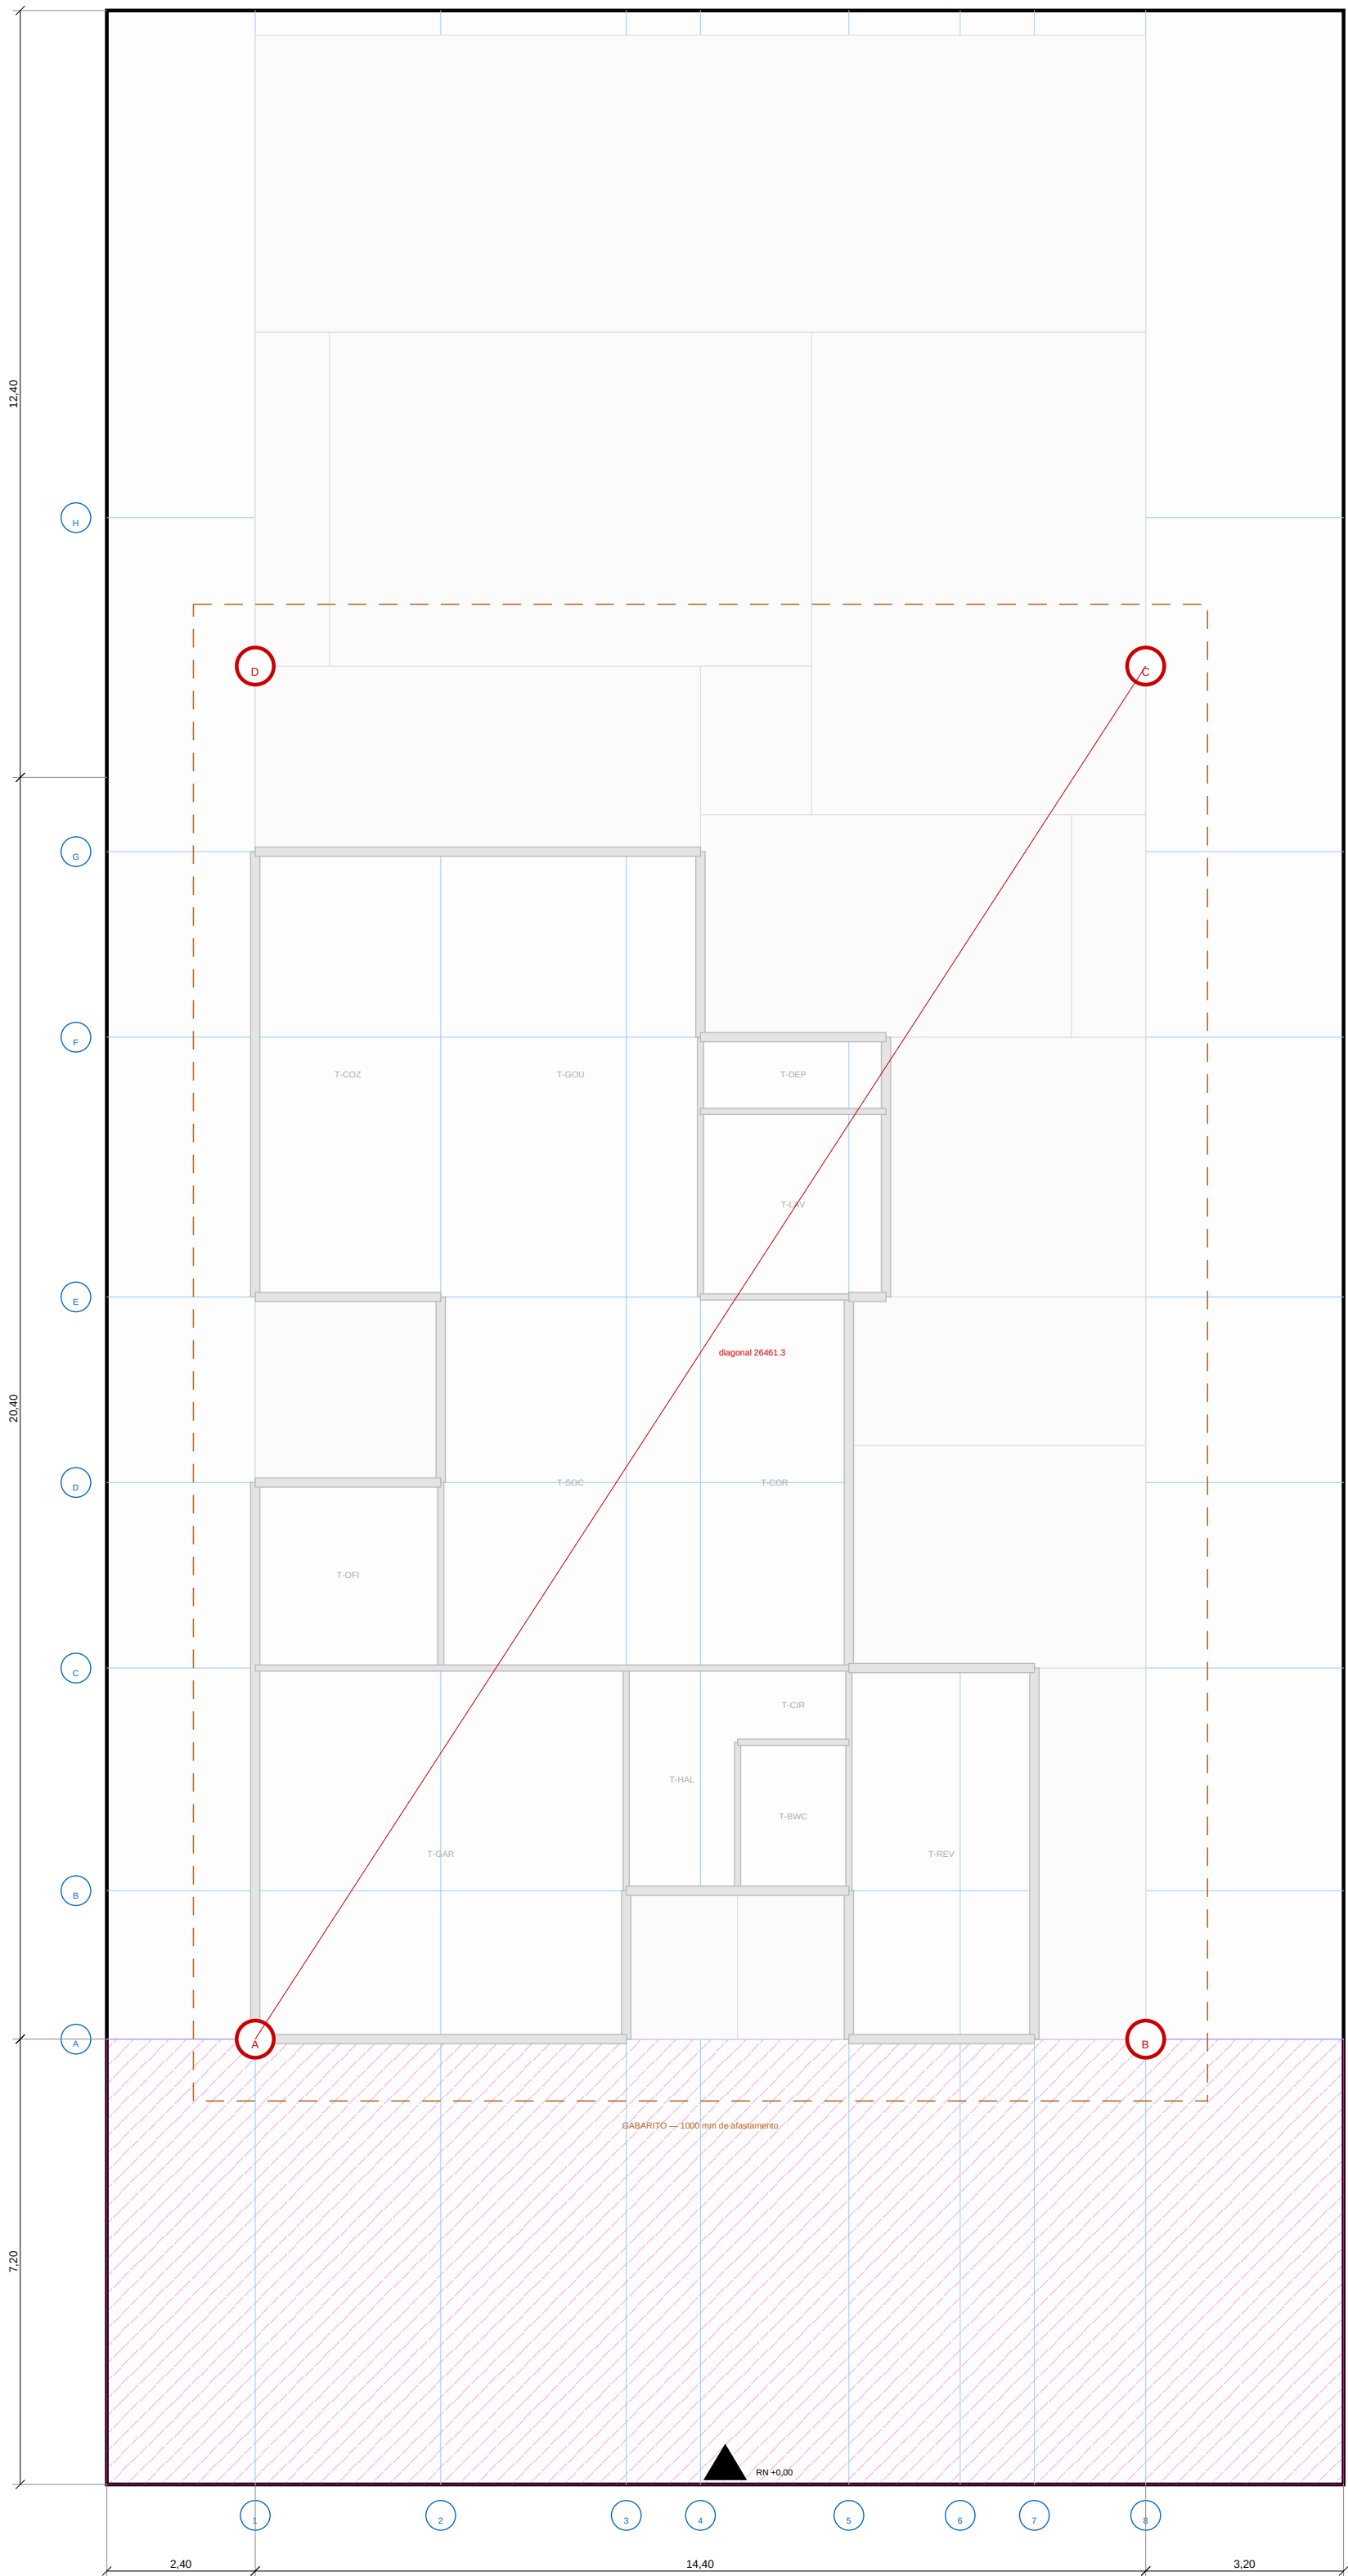

COORDENADAS DOS CANTOS (mm)

CANTO	X	Y	DISSA-ALA	DISSA-NORTE	TESTADA	FORNO	DIAGONAL
A	2400	7200	2400	17600	7200	32800	26461,3
B	18800	7200	18800	3200	7200	32800	26461,3
C	18800	28400	18800	3200	28400	19600	26461,3
D	2400	28400	2400	17600	28400	19600	26461,3

PROCEDIMENTO DE LOCACAO

#	PASSO	CRITERIO DE ACABO
1	Conferir as divisões com a malha e o material de base	divergência acima de 10 mm interromper a locação
2	Instalar o PIM (marco de concreto 200 x 200 x 100 mm, fora da área de obra)	fora da área de obra
3	Montar o gabarito a 1000 mm do cantoneiro	pergunte 75 x 75 a 100 x 100
4	Marcar os eixos X (1 a 5) e Y (A a E) no gabarito	linha coordenada múltipla de 200 mm
5	Cortar cabos com os OLARS diretos	retirar em cabos; erro de cabos soma
6	Conferir a diagonal A-C	26461,3 mm com tolerância de 20 mm
7	Conferir o quadrado por 3-4-5 em cada canto	antes de qualquer concretagem
8	Registrar em ata com foto e modelo	gabarito continuo nos dois lados da obra, conferindo

EIXOS MODULARES

DIRECAO	MODULO (mm)
X (1 a 5)	2400 5400 8400 9600 12000 12800 15000 16800
Y (A a E)	7200 9600 13200 14000 15000 28400 29400 32800
Malha	principal 600 mm - subgrid 300 mm
Origem	canto frontal esquerdo da base
Unidade	milímetros

NOTAS

- Locação é o único documento em que o erro não tem contorno técnico: a casa sai do lugar.
- Cada canto é o coteado dos OLARS diretos, nunca em cabos acumulados — erro de cabos soma, erro de referência independente não.
- Conferência obrigatória pela diagonal 26461,3 mm entre A e C antes de concretar o radier.
- Ata ou livro de locação, assinado por todos os envolvidos (TC-OB, caso OLAR) e pelo acurado do terreno.

PROJETO PORTO REAL

RESIDENCIA UNIFAMILIAR (MANAUS - AM) | SOBR TATIANA-PS

PROJETO ARQUITETONICO

LOCACAO DE OBRA E GABARITO

BASE GEOMETRICA Linha Consolidada Projeto (previsão) UNIDADE: METRO - MM	ESCALA 1:100 FORMATO A1 MALHA: 600/300/300	DISSAIO ESTUDO PRELIMINAR R3B LIVRO LIBERADO PARA OBRA SEM ART / RNT	PROJETA 31 06-25 REV-03B
---	--	---	---------------------------------------