
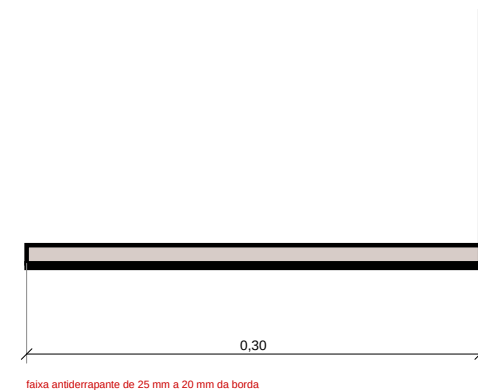
 
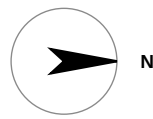


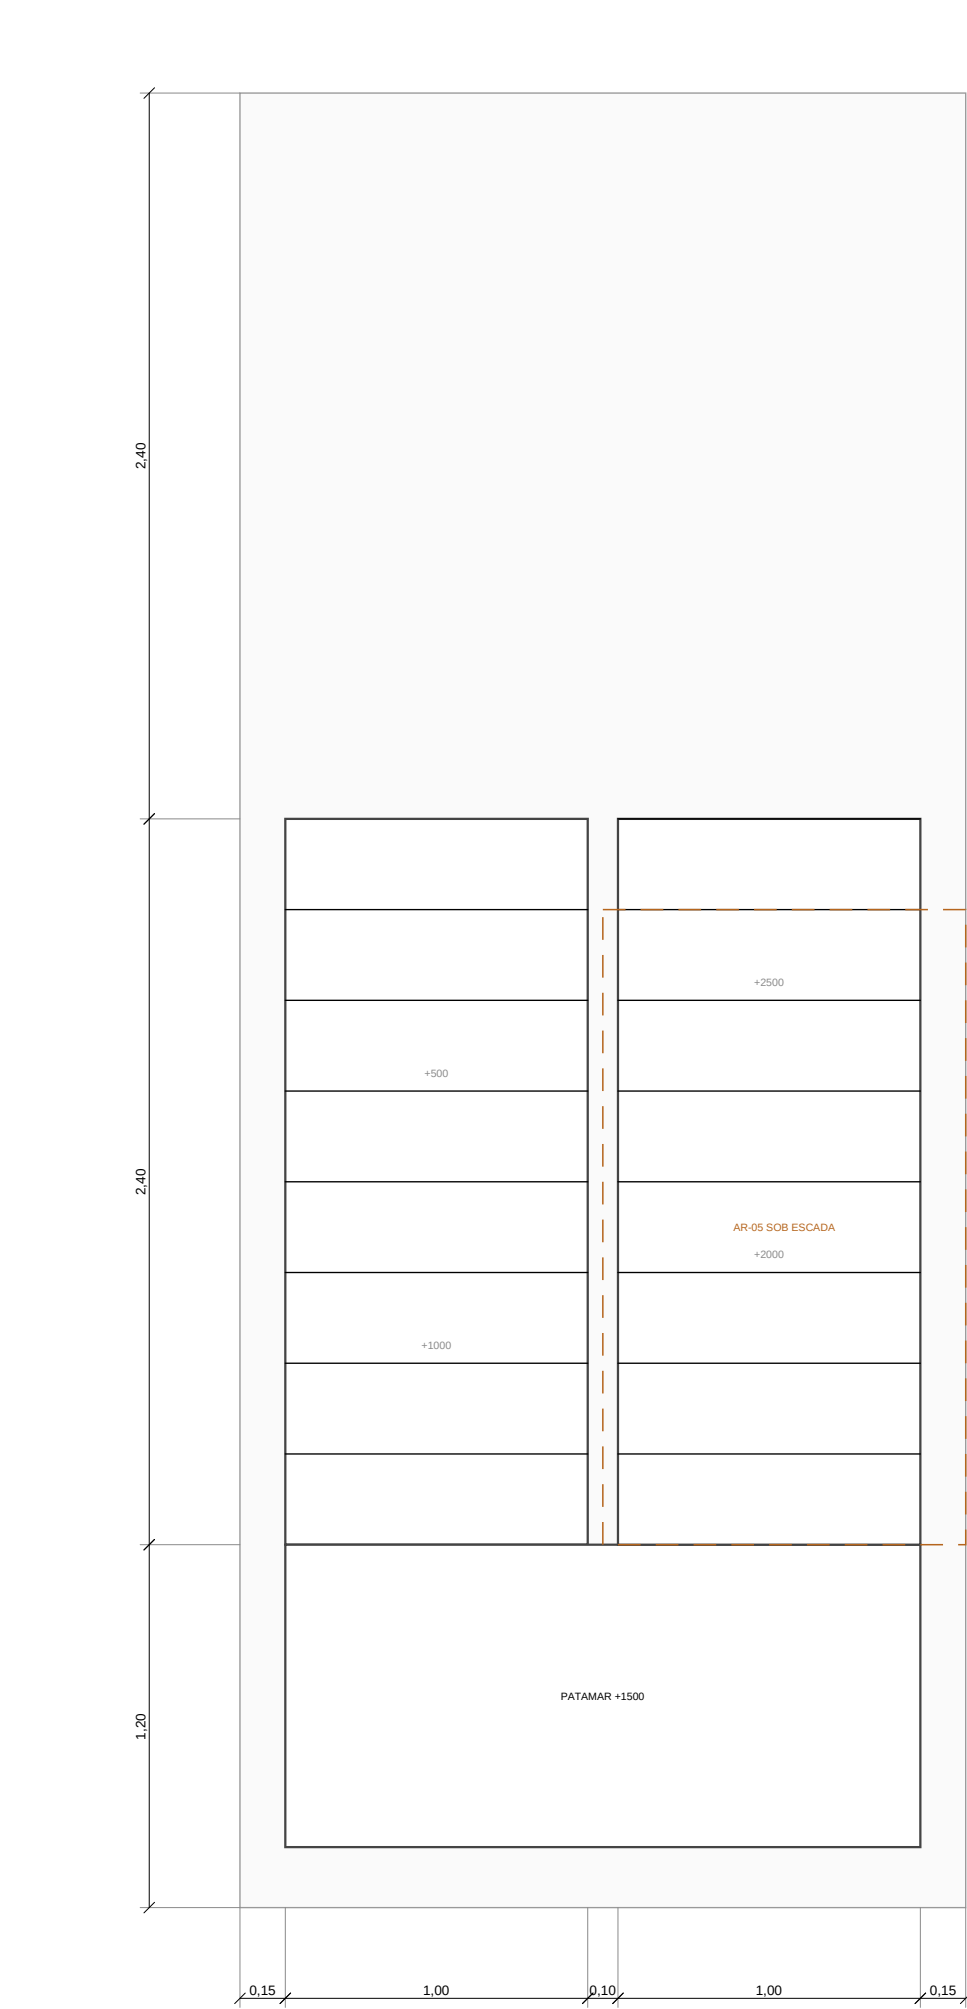

espelho fechado (NBR 9050)

chapa 80x80x3 mm - preenchido 90x x 300

1 PLANTA DA ESCADA

ESCALA 1:25

VERIFICACAO DA ESCADA

ITEM	PROPOSTO	NORMA	
Espelho	186,67 mm	18 a 18 cm (NBR 9077)	OK
Piso	300 mm	min 28 cm	OK
Bondex (2h + g)	633,3 mm	600 a 650 mm	OK
Largura útil do lance	1000 mm	min 1.200 mm (para cobrir) e 1.300 mm (para ficar)	OK
Platamar	1000 mm	min largura do lance	OK
Altura livre mínima	0 mm	min 2100 mm	EXCETO
Guarda-corpo	1100 mm	min 1.200 mm (NBR 14738)	OK
Corrimão	920 x 700 mm	Acabado 92 cm x 70 cm (NBR 9050)	OK
Espelho fechado	sem	congelamento em sala acustica	OK
Desnível verificado	3000 mm	18 x 186,67 mm	OK

O QUE A PLANTA NAO MOSTRA

QUESTAO	RESPOSTA
Por que o primeiro espelho sobre o y é 18,667?	o primeiro tem 186,67 mm dentro da projeção do 1º degrau, com 1.000 mm de altura livre — então quanto a altura da cobertura do quem tem o primeiro lance
Por que a verificação de altura livre é bidimensional?	altura livre da escada e o único critério que não aparece em planta horizontal, dependendo da cor do degrau e da cor do que há acima dele
O que há sob o segundo lance?	intergelo com altura útil variável, deslizada como amarra (pelo 050) mas a circulação tem espaço morto
Por que espelho fechado?	alguma vez você prende a porta do pé de quem está chegando ou tem mobilidade reduzida (NBR 9050)
Por que corrimão duplo?	920 mm para adulto e 700 mm para criança, em caso com escada aberta para a sala, o segundo corrimão é o que realmente se usa

NOTAS

- 18 espelho de 186,67 mm e piso de 300 mm. Bondex 2h + g = 633,3 mm (falso recomendado 600 a 650).
- Altura livre mínima 2100 mm (NBR 9077), verificada diagonal a degrau contra a tape e o resto acima.
- Guarda-corpo 1100 mm, corrimão duplo em 920 x 700 mm (NBR 9050).
- dois perfis U 200 laterais com degraus em chapa aluminada 3 mm.

PROJETO PORTO REAL

RESIDENCIA UNIFAMILIAR (MARAUAS - AM) | 500x700MM-PS

PROJETO ARQUITETONICO

ESCADA — DESENHO EXECUTIVO

BASE GEOMETRICA	ESCALA	EMISSAO	PROVA
Unidade Consolidada	indicada	ESTUDIO PRELIMINAR R08	25
Projeto (previsão)	FORMATO A1	NAO LIBERADO PARA OBRA	em 25 REVIZOES
Unidade (previsão)	MAQUETA 600x900mm	SEM ART / PRINT	