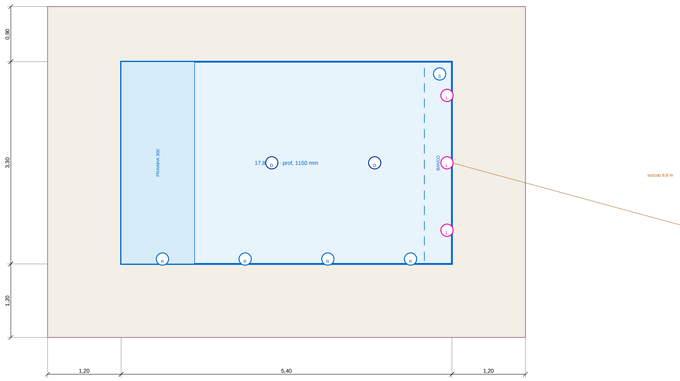

1 **PISCINA E DECK**
ESCALA 1:50

succao 6.8 m

TC-13

PISCINA — GEOMETRIA E SISTEMA

ITEM	PROJETO	ORIGEM / RAZAO
Dimensao da lamina	5400 x 3300 mm	YAML pede 5,50 x 3,20; adotado modular, mesma area util
Area / volume	17,82 m2 / 17,13 m3	volume dentro da faixa de 17 a 19 m3 do YAML
Profundidade	1150 mm	faixa 1,10 a 1,20 do YAML
Prainha	1200 mm x 300 mm	entrada rasa, area de permanencia de crianca
Banco submerso	450 x 450 mm	borda oposta a prainha, sem reduzir o vao de nado
Faixa seca	min 900 mm nos 4 lados	exigencia do YAML, verificada pela auditoria
Recirculacao	2,85 m3/h em 6 h	bomba de velocidade variavel: gasta menos rodando devagar mais tempo
Drenos de fundo	2 un., antiaprisionamento	dois drenos de fundo afastados 900 mm sao exigencia antiaprisi
Retornos / skimmer / aspiracao	4 / 1 / 1	retornos opostos ao skimmer, para varrer a superficie
Iluminacao	3 LED de 18 W, 2700-3000 K	luz quente: agua azul com luz fria fica enverdeada
Aquecimento	nao instalado; bypass e espaco de trocador previstos	bypass custa dois registros hoje, abrir piso depois custa a obra
Tratamento	cloro convencional; sal em espera (HOLD no YAML)	sal exige material compativel em TODA a hidraulica; decisao em espera

DECK — PISO POR ZONA, NAO POR MATERIAL UNICO

ZONA	MATERIAL	RAZAO
faixa seca da piscina	porcelanato externo claro R11	e onde se anda descalco no pico do sol
lounge e circulacao do deck	WPC cinestruturado claro	area de permanencia com mobiliario e sombra
passeio e acesso	piso drenante intertravado claro	compensa a permeabilidade perdida pelo deck
Verificacao do YAML	aquecimento superficial	WPC escuro passa de 65 C sob sol de Manaus (albedo 0,20); porcelanato claro fica em ~45 C (albedo 0,60), a dor ao pe descalco comeca em 50 C

FACHADA — TRES FAMILIAS E O RASGO DE LUZ

FAMILIA / ELEMENTO	ESPECIFICACAO	EFEITO
Mineral claro de grande formato	placa cimenticia com revestimento mineral 1.200 x 2.400, junta seca de 6 mm	—
Aluminio grafite ripado	portao de correr, lerias e guarda-corpo	—
Madeira	folha da porta de entrada e forro do portico	—
IF-01 — reentrancia do portico de entrada	perfil linear LED IP65, 2.700 K, 8 W/m, embutido no forro	lava a folha de madeira da porta e marca a profundidade do portico
IF-02 — sob o beiral do volume superior	perfil linear LED IP65, 2.700 K, 8 W/m	risco horizontal continuo: e ele que faz a casa parecer baixa e longa a noite
IF-03 — base do muro e do portao ripado	balizador embutido no piso, 3 W, feixe rasante	revela a textura do ripado por raspagem
IF-04 — uplight nas palmeiras da entrada	projetor de solo 7 W, 2.700 K, feixe 15 graus	profundidade: a copa iluminada recua o plano de fundo

O QUE A REFERENCIA VISUAL CONFIRMOU E O QUE ACRESCENTOU

LEITURA	SITUACAO NO PROJETO
Composicao horizontal, volumes escalonados	ja era o partido: garagem em um pavimento, portico recuado, corpo de dois pavimentos atras
Revestimento mineral claro de grande formato	familia 1 ja especificada; junta seca de 6 mm mantida
Portas e brises ripados em metal escuro	familia 2 ja especificada — e agora tambem sombreia o nicho de condensadoras, no lugar da trelica vegetal
Porta pivotante alta em madeira	familia 3; PD1 de 1.100 x 2.800 mm ja previa a folha alta
Rasgo de luz indireto sob cada plano	ACRESCENTADO nesta revisao (IF-01 a IF-04): e o que constroi a horizontalidade a noite
Palmeiras de grande porte na entrada	compativel com o paisagismo sem poda; uplight IF-04 previsto
Piso claro refletindo a iluminacao	coincide com a decisao tomada por desempenho termico: albedo alto no piso externo

NOTAS

- Piscina 5,40 x 3,30 m = 17,82 m2 de lamina, 17,13 m3, O YAML fixa 5,50 x 3,20; adotado modular sobre a malha de 300 mm,
- Faixa seca perimetral minima 900 mm, verificada nos quatro lados.
- Recirculacao 2,85 m3/h para renovar o volume em 6 h,
- Fachada: tres familias de material, confirmadas pela referencia visual; a novidade e o rasgo de luz indireto.

PROJETO PORTO REAL

RESIDENCIA UNIFAMILIAR | MANAUS - AM | SUB3 TARUMA (H)

PROJETO ARQUITETONICO

PISCINA, DECK E FACHADA — REVISAO R06

BASE GEOMETRICA	ESCALA	EMISSAO	PRANCHA
Lista Consolidada pos-R32 (prevalece)	indicada	ESTUDO PRELIMINAR R28 NAO LIBERADO PARA OBRA	34
UNIDADE MESTRE: mm	FORMATO A1 MALHA 600/300/150	SEM ART / RRT	de 35 REV R28