
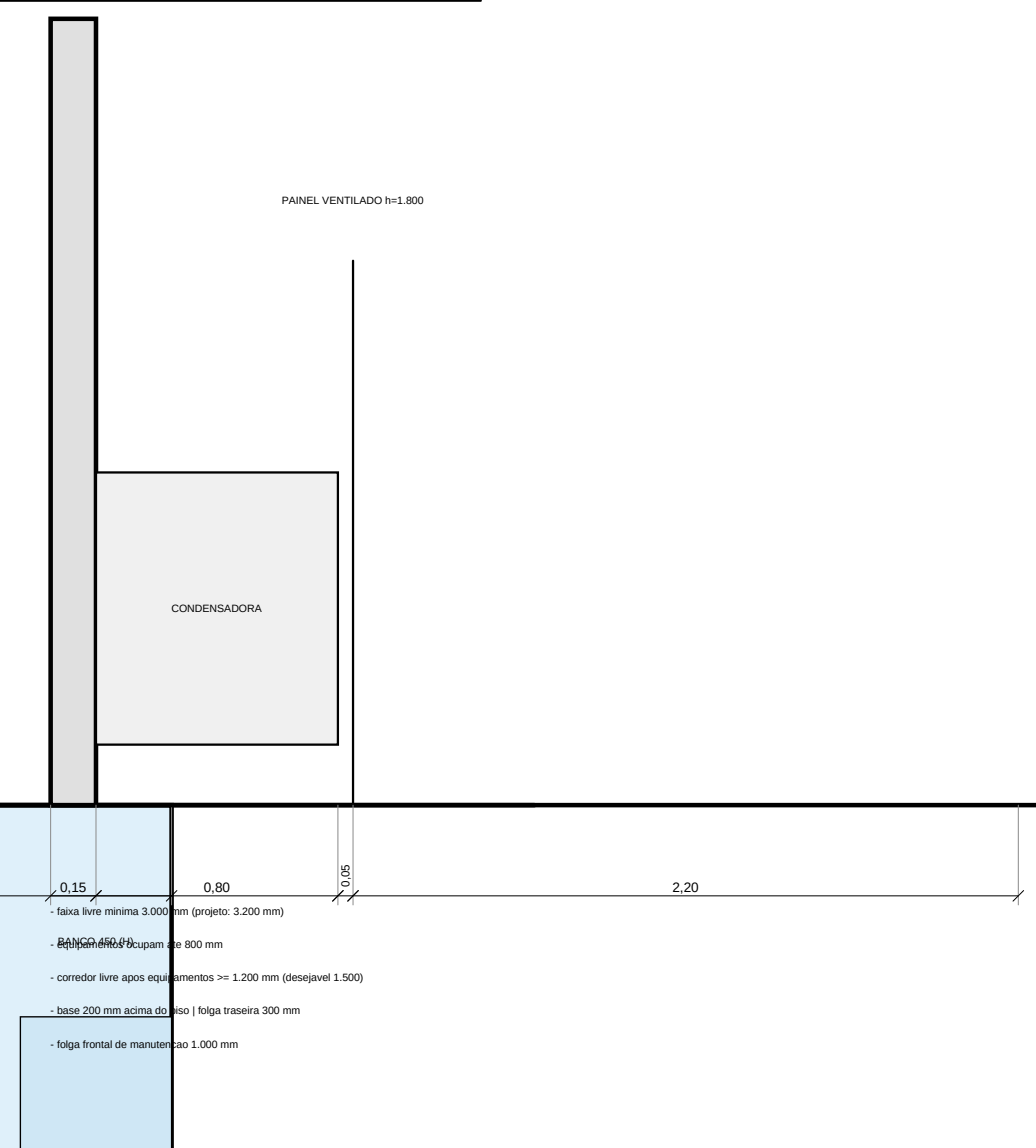


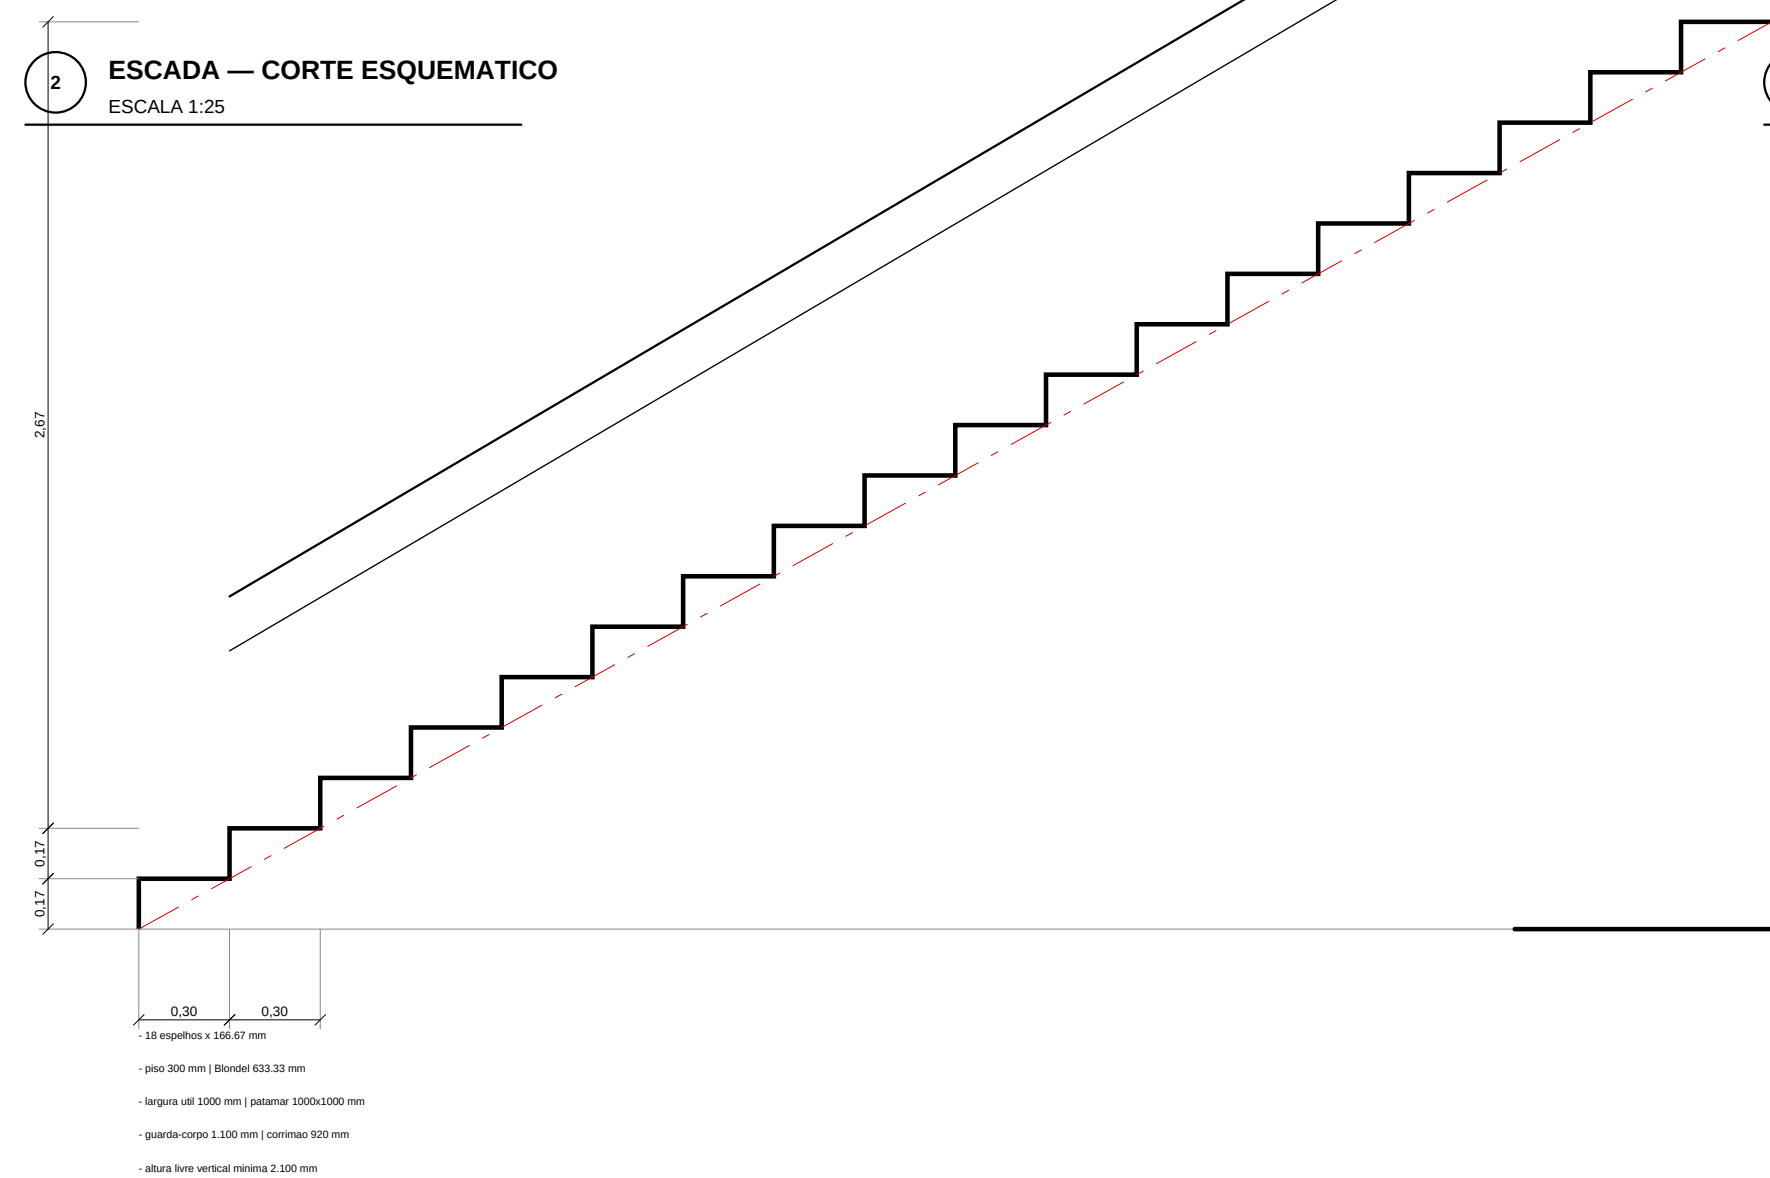

- Detalhes de estudo — não liberados para fabricação ou corte (sem nesting codificado).
- Parede externa consolidada em 150 mm; divisória interna em 100 mm (H).
- Escada reconciliar com estrutura, guarda-corpo e espessura de acabamento antes de definitiva.

PROJETO PORTO REAL RESIDENCIA UNIFAMILIAR (MANAUS - AM) (SOLTA TAMBORA 05)			
PROJETO ARQUITETONICO DETALHES CONSTRUTIVOS AMPLIADOS			
BASE GEOMETRICA Linha Consolidada pos-R22 (provisoria) USUÁRIO MESTRE: AM	ESCALA indicada FORMATO A1 MILIMETROS 5000/3000	ENTRADA ESTUDO PRELIMINAR R305 NÃO LIBERADO PARA OBRA SEM ART / IMPR	FUNÇÃO 10 05.10 REV R305