




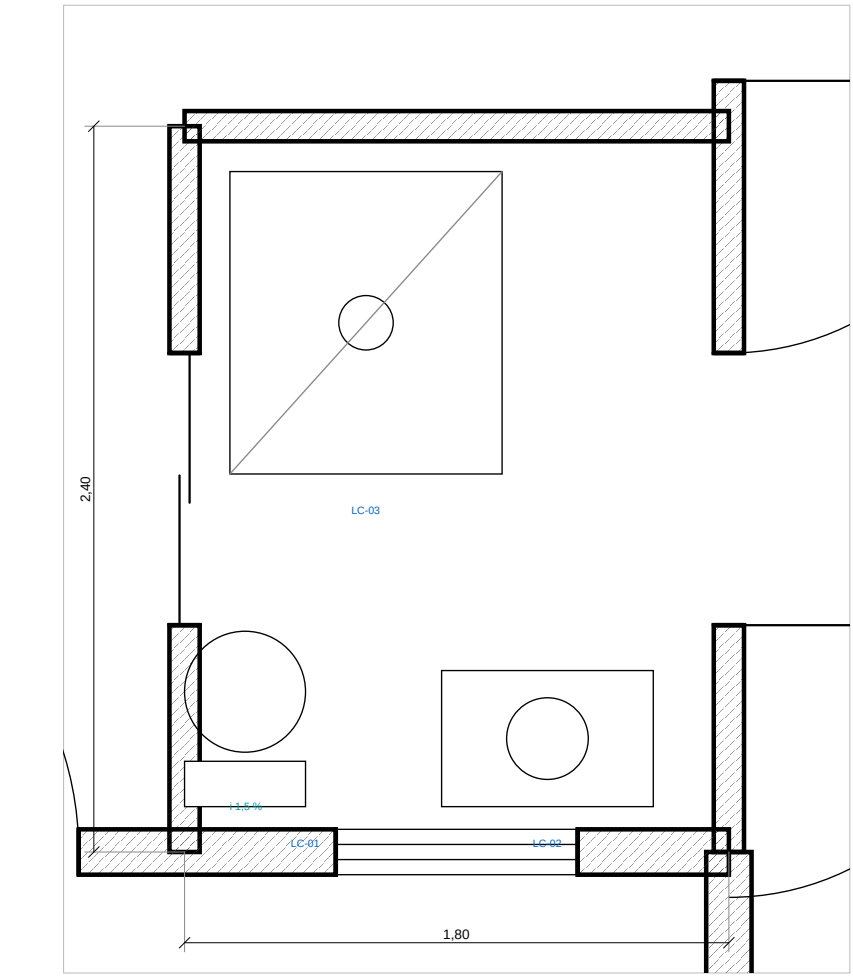


1 BANHO SOCIAL
ESCALA 1:25

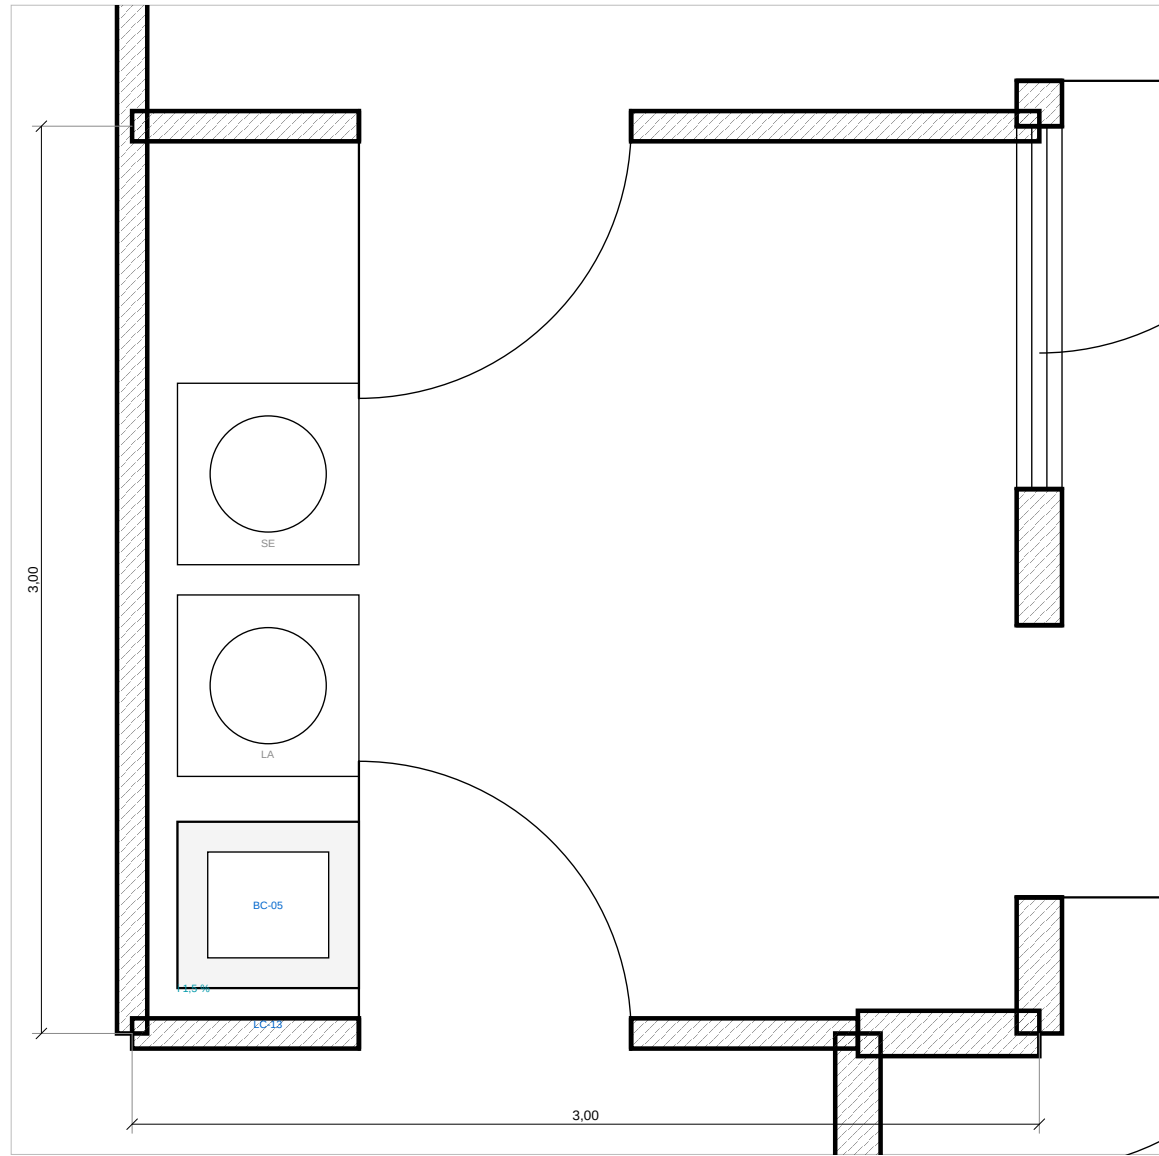

2 LAVANDERIA
ESCALA 1:25

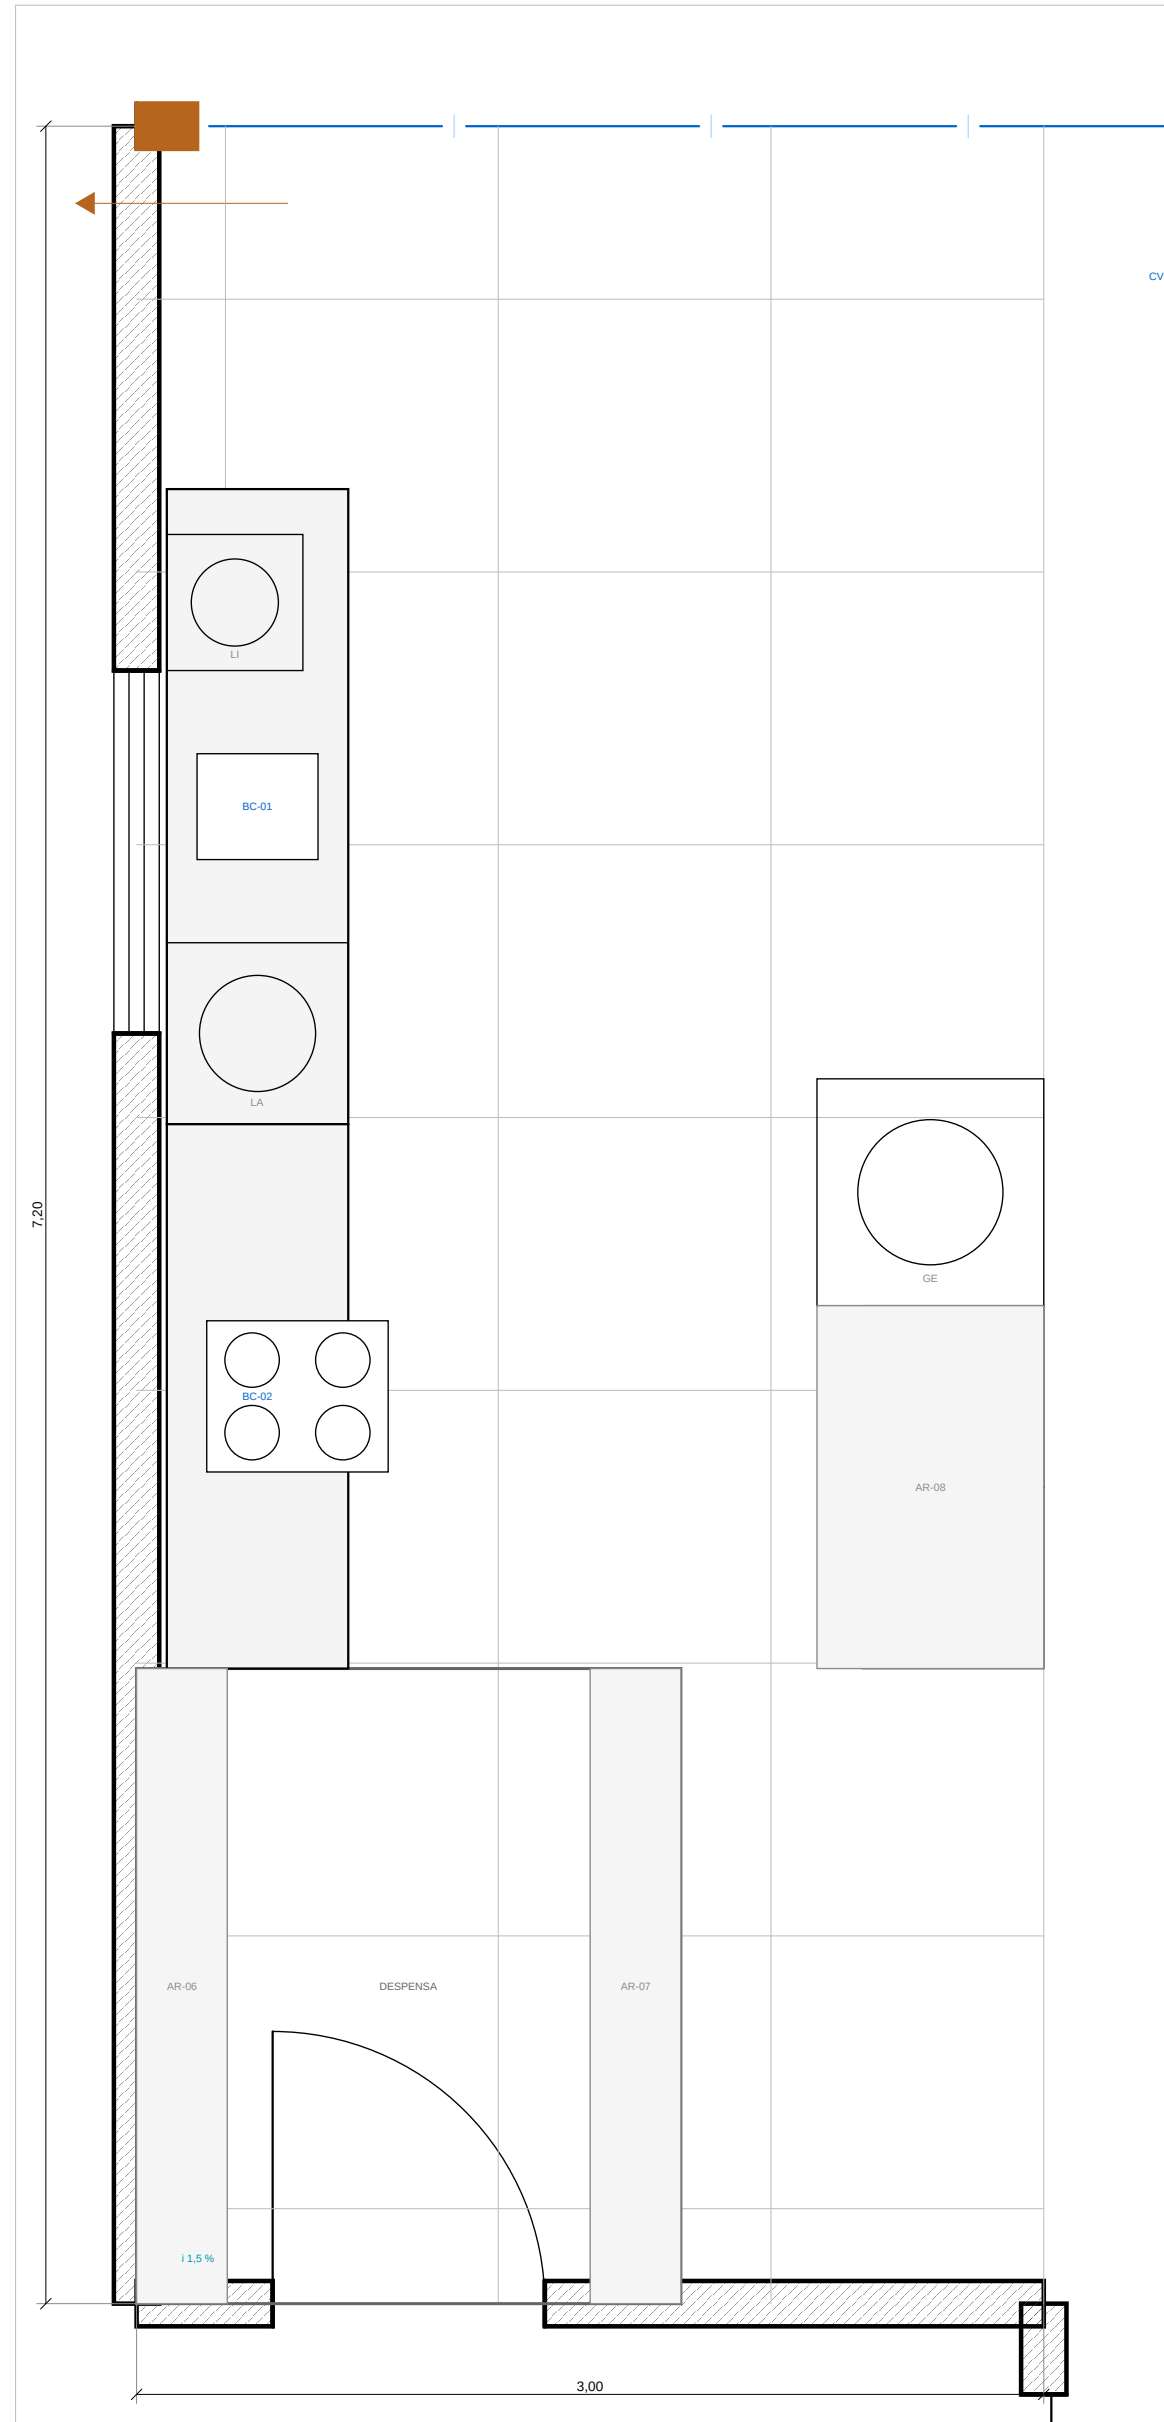

3 COZINHA
ESCALA 1:25

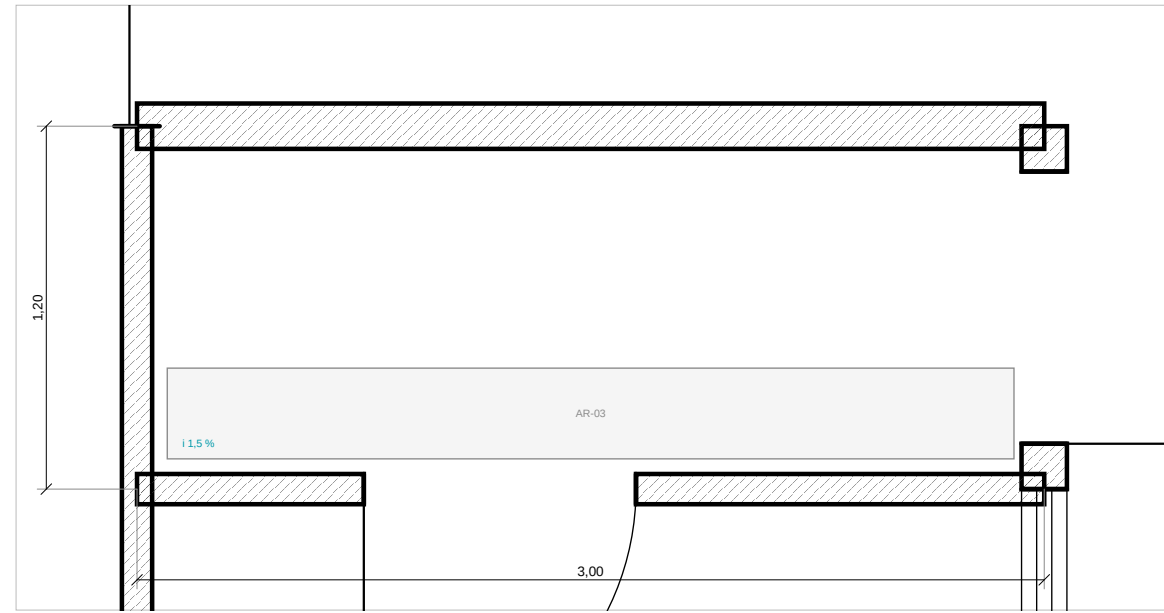

4 DEPOSITO / DML
ESCALA 1:25

PAGINACAO VERIFICADA — PECAS INTEIRAS + RECORTE EM CADA PONTA

AMB	AMBIENTE	ZONA	PEÇA	EXO X	EXO Y	ALTURA (mm)
T-BWC	BANHO SOCIAL	ZP-4	parede	0 + 0200	0 + 0000	2400 (2 Ruas + 100)
T-LAV	LAVANDERIA	ZP-5	parede	0 + 0200	4 + 0500	2400 (2 Ruas + 100)
T-COC	COZINHA	ZP-1	pis	0 + 0200	7 + 112010	—
T-DEP	DEPOSITO / DML	ZP-5	parede	0 + 0200	1 + 0500	2400 (2 Ruas + 100)

NOTAS

- * Pignoneus de piso em linha fina, a malha vem da ZONA de pignoneus, não do canto do ambiente.
- * Peca de piso porcelanado retificado 900 x 900, parede ceramico retificado 300 x 600, junta 2 mm.
- * Caminho de 1.5 % para o lado em toda area molhada, solteira elevada 15 mm nos bicos.
- * Representação: marra lquida em 2 dimensoes, subido 300 mm na parede e 1.800 mm nos bicos.

PROJETO PORTO REAL

RESIDENCIA UNIFAMILIAR (MANAUS - AM) | SOUZA TATIANA-PS

PROJETO ARQUITETONICO

AMPLIACOES DE AREA MOLHADA — TERREO

BASE GEOMETRICA Linha Consolidada Projeto (previsão) UNIDADE: METRO - MM	ESCALA 1:25 FORMATO A1 MILHA 400/500/500	EXIBICAO ESTUDIO PRELIMINAR R06 LIMBO LIBERADO PARA OBRAS SEM ART / RNT	PROJECION 22 06-25 REV-005
---	---	--	----------------------------------