
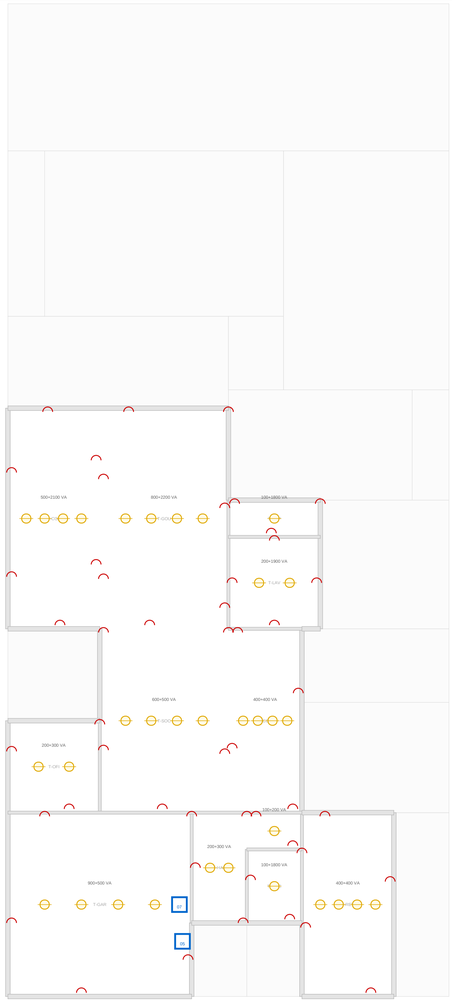


1 PONTOS ELETRICOS — TERREO

ESCALA 1:100

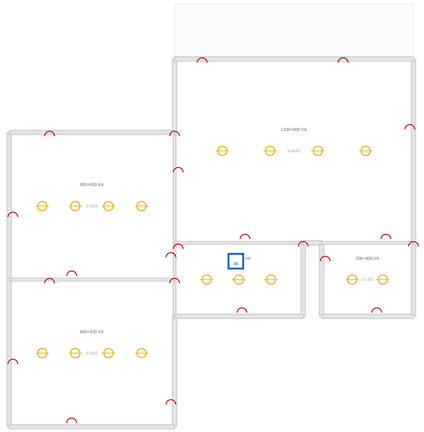

2 PONTOS ELETRICOS — SUPERIOR

ESCALA 1:100

QUADRO DE CARGAS E DEMANDA

COD	CARGA	VA	TENSAO	GRUPO	fd	DEMANDA (VA)
TUE-1	Chuveiro eletrico suite master	4.500	220 V	aquecimento	0,75	3.375
TUE-2	Chuveiro eletrico suite 02	4.500	220 V	aquecimento	0,75	3.375
TUE-3	Chuveiro eletrico suite 03	4.500	220 V	aquecimento	0,75	3.375
TUE-4	Chuveiro eletrico banho social	4.500	220 V	aquecimento	0,75	3.375
TUE-5	Split duto 30.000 BTU (zona social)	2.300	220 V	climatizacao	1,00	2.300
TUE-6	Split 18.000 BTU suite master	1.400	220 V	climatizacao	1,00	1.400
TUE-7	Split 18.000 BTU suite 02	1.400	220 V	climatizacao	1,00	1.400
TUE-8	Split 18.000 BTU suite 03	1.400	220 V	climatizacao	1,00	1.400
TUE-9	Split 18.000 BTU quarto reversivel	1.400	220 V	climatizacao	1,00	1.400
TUE-23	Split 9.000 BTU mini sponge	800	220 V	climatizacao	1,00	800
TUE-24	Split 9.000 BTU office da master	800	220 V	climatizacao	1,00	800
TUE-25	Bomba piscina 1/2 cv	2.700	220 V	servico	0,50	1.350

PREVISAO DE CARGA POR AMBIENTE (12 MAIORES)

AMB	AMBIENTE	AREA	PERIM (m)	ILUM (VA)	TUG	TUG (VA)	CLASSE
S-MAS	SUITE MASTER	46,80	27,6	1200	6	600	seca
T-GAR	GARAGEM	36,00	24,0	900	5	500	seca
T-GOU	GOURMET	30,24	22,8	900	7	2200	molhada
S-SI2	SUITE 02	25,92	20,4	600	5	500	seca
S-SI3	SUITE 03	25,92	20,4	600	5	500	seca
T-SOC	ESTAR / JANTAR	25,20	20,4	600	5	500	seca

(continuacao)

AMB	AMBIENTE	AREA	PERIM (m)	ILUM (VA)	TUG	TUG (VA)	CLASSE
T-COZ	COZINHA	21,60	20,4	900	6	2100	molhada
T-REV	QUARTO REVERSIVEL	18,00	18,0	400	4	400	seca
T-COR	CORE / ESCADA	14,40	16,8	400	4	400	seca
S-HAL	HALL E ROUPARIA	10,08	13,2	300	3	300	seca
T-OFI	OFICINA	9,00	12,0	200	3	300	seca
T-LAV	LAVANDERIA	9,00	12,0	200	4	1900	molhada

(continuacao) POR QUE fd = 1,00 NA CLIMATIZACAO

COD	CARGA	ARGUMENTO	DESENVOLVIMENTO
TUE-12	Lava-louca		
TUE-13	Forno eletric	O que a tabela assume	os fatores de demanda da NBR 5410 vem de media nacional, onde ar condicionado e carga intermitente e sazonal
TUE-14	Micro-ondas		
TUE-15	Motobomba	O que acontece em Manaus	os cinco equipamentos funcionam juntos em todas as tardes do ano, nao existe a diversidade que o fator pressupoe
TUE-16	Pressurizad		
TUE-17	Bomba x fil	O que custa errar	com fd 0,70 a demanda cairia 2.370 VA e o padrao desceria de 100 A — o ramal aquece e o disjuntor geral desliga exatamente na hora de maior calor
TUE-18	Ventilador	O que o proprietario faria	trocaria o disjuntor por um maior em vez do cabo, transformando uma protecao em um risco de incendio
TUE-19	Exaustores	Custo de acertar	cabo de 35 mm2 em vez de 25 mm2 no ramal de entrada: dezenas de metros, uma vez na vida da casa
TUE-20	Portao automatico		500 220 V diversos 0,30 150
TUE-21	Rack, CFTV e rede		300 127 V diversos 1,00 300
TUE-22	Carregador de veiculo eletrico (INFRAESTRUTURA		7.400 220 V reserva 0,00 0
TUE-26	...	Iluminacao + tomadas de uso geral	22.000 127 V base 0,24 5.280
			36.400

NOTAS

- Previsao de carga conforme NBR 5410 B.5.2. Instalada 70.350 VA; demanda provavel 36.400 VA.
- Entrada trifasica 127/220 V (N); 95,5 A -> padrao 100 A com cabo de 35 mm2.
- Fator de demanda do ar condicionado adotado 1,00 — em Manaus ele e carga continua, nao intermitente. Ver justificativa no quadro.
- Quadro geral Quadro geral 36 modulos na garagem; quadro do superior no hall.

PROJETO PORTO REAL

RESIDENCIA UNIFAMILIAR | MANAUS - AM | SUB TARUMA (H)

PROJETO ARQUITETONICO

ELETRICA, ILUMINACAO E DADOS

BASE GEOMETRICA	ESCALA	EMISSAO	PRANCHA
Lista Consolidada pos-R32 (prevalece) UNIDADE MESTRE: mm	1:100 FORMATO A1 MALHA 600/300/150	ESTUDO PRELIMINAR R36 NAO LIBERADO PARA OBRA SEM ART / RRT	27 de 35 REV R36