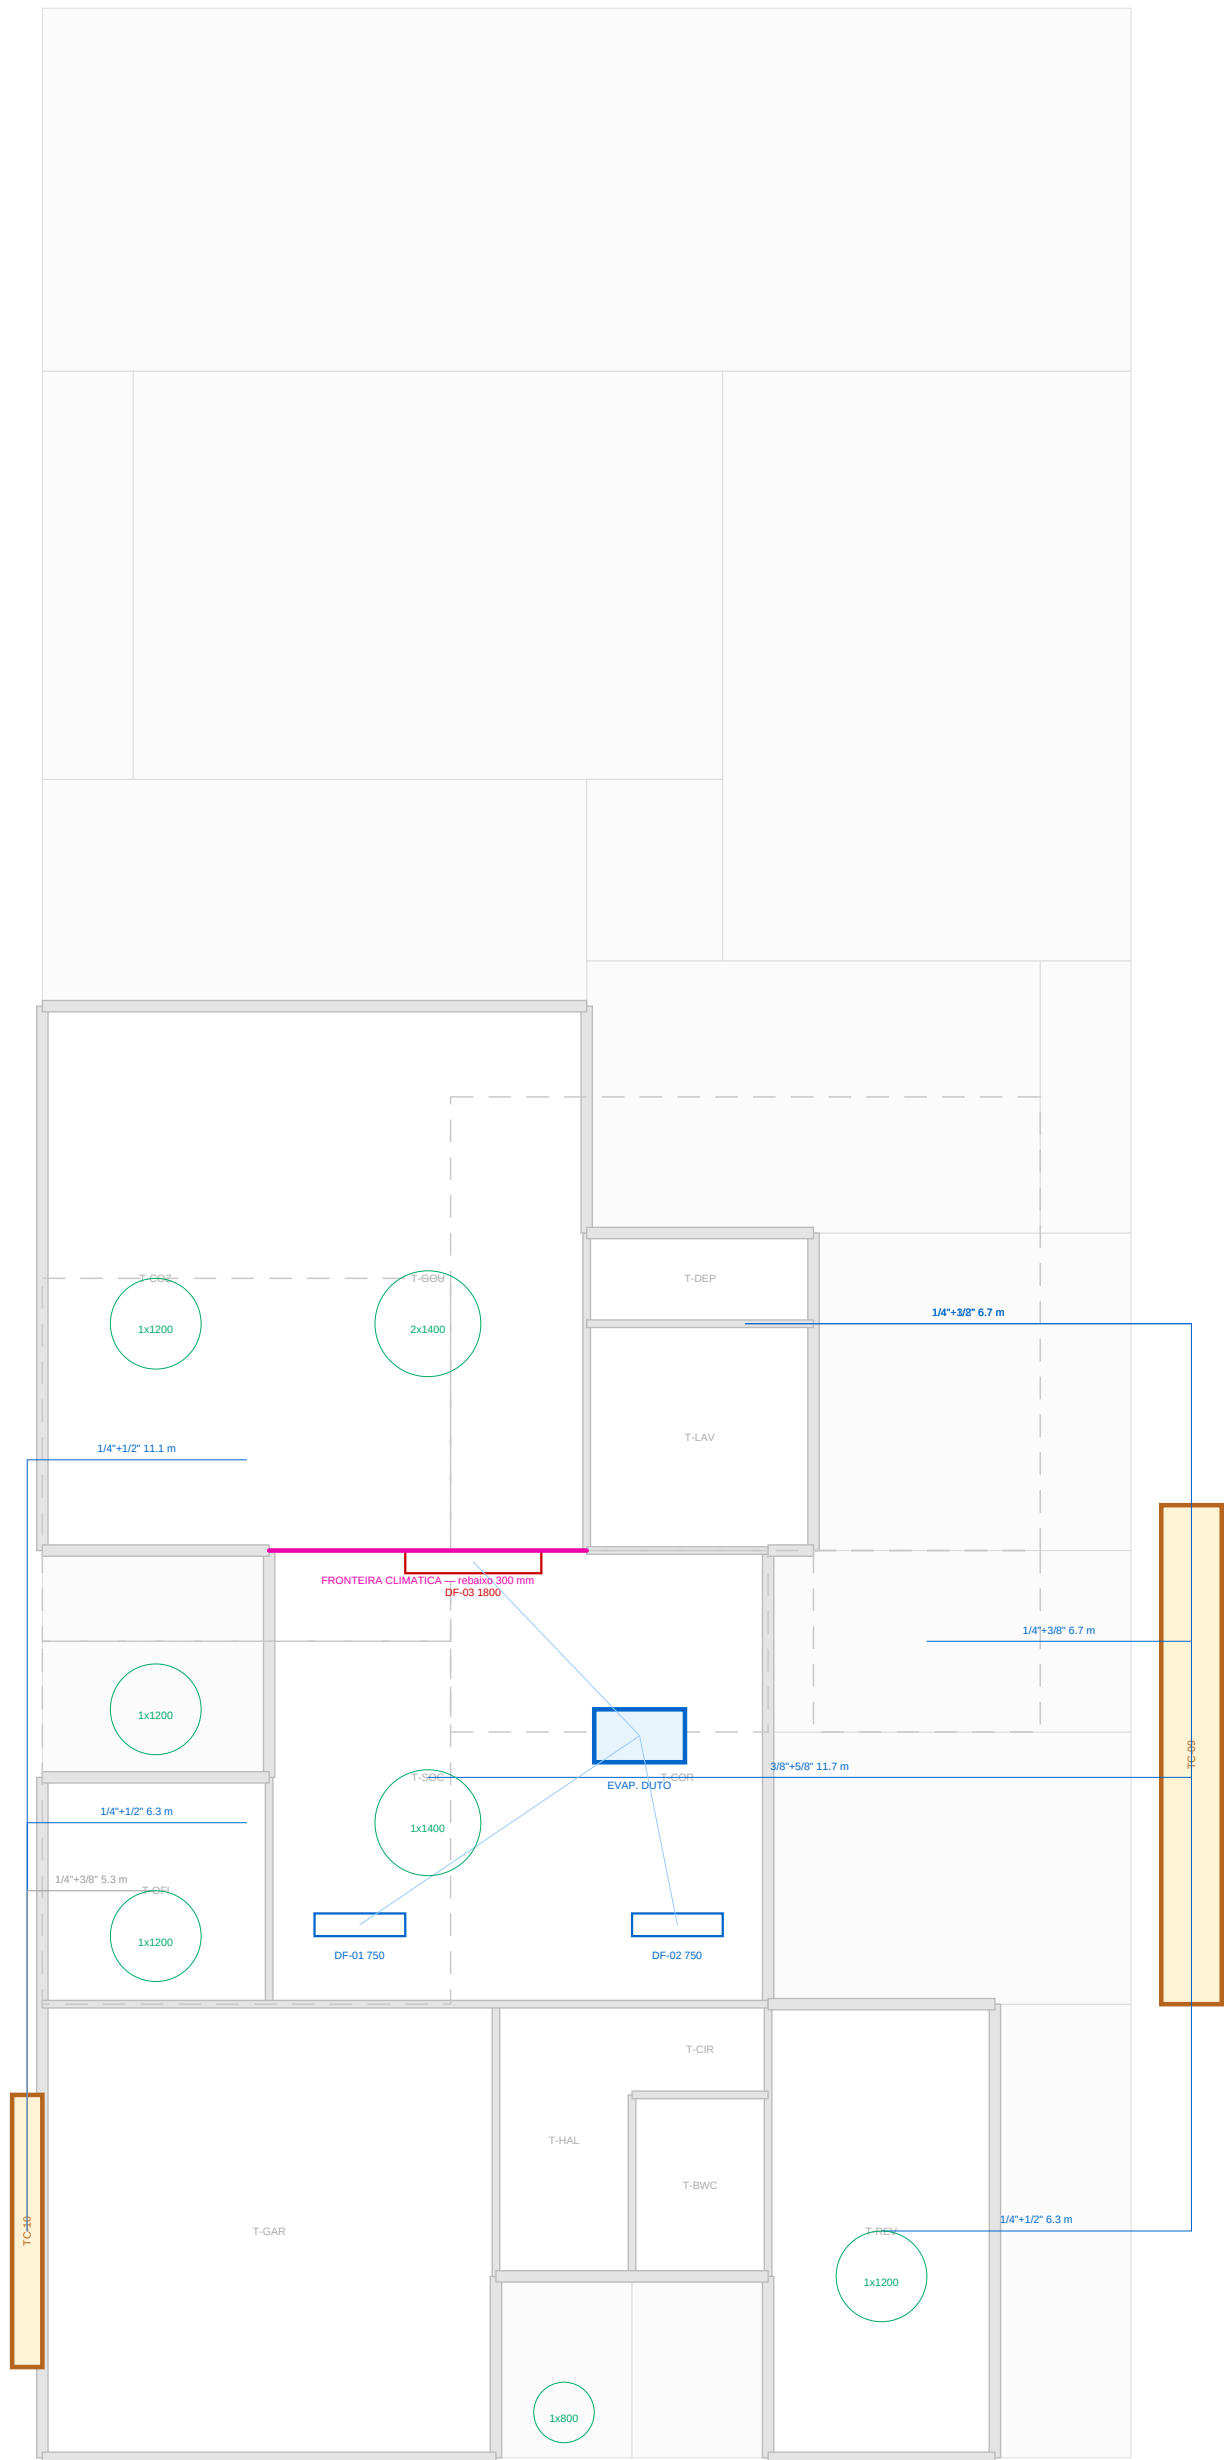


1 PERCURSO DAS LINHAS E DUTOS
ESCALA 1:100

LINHAS FRIGORÍGENAS — PERCURSO E BITOLA

Linha	AMB	INCHO	BTUM	HORIZ (m)	VERTIC (m)	TOTAL (m)	SUCCASOLU	DRENOS	CARGA EXTRA	FASE
S-001	S-001	TC-01	18.000	1,6	3,8	6,7	1/4" x 1/2"	DN25	—	ABR
T-REV	T-REV	TC-01	18.000	2,2	2,6	6,3	1/4" x 1/2"	DN25	—	ABR
S-002	S-002	TC-10	18.000	1,2	3,6	6,3	1/4" x 1/2"	DN25	—	ABR
S-003	S-003	TC-10	18.000	6,0	3,6	11,1	1/4" x 1/2"	DN25	R2 g	ABR
S-004	S-004	TC-08	20.000	1,6	2,8	11,7	3/8" x 1/2"	DN25	R2 g	ABR
S-005	S-005	TC-08	9.000	1,6	3,8	6,7	1/4" x 3/8"	DN25	—	ABR
FFCE	S-005	TC-08	9.000	1,6	3,8	6,7	1/4" x 3/8"	DN25	—	ABR
T-001	T-001	TC-10	9.000	1,2	2,8	5,3	1/4" x 3/8"	DN25	—	ABR

DUTOS, DIFUSORES E EXAUSTÃO

ELEMENTO	VIAJADA (mm)	DNOM	OBSERVAÇÃO
DP-01 — insulflex	750	T-001	para parede sobre do motor
DP-02 — insulflex	750	T-001	com, sob o piso de faz

(continuação)

ELEMENTO	VIAJADA (mm)	DNOM	OBSERVAÇÃO
EX-01 — BENTO 5000	85	T-001	DN25
EX-02 — BENTO 5000	105	T-001	DN25
EX-03 — BENTO 5000	125	T-001	DN25
EX-04 — BENTO 5000	145	T-001	DN25

- NOTAS
- Dots rictos de condensação. Linha mais longa 11,7 m, contra o limite de contorno de 15 m.
 - Drenos DN25 com diâmetro mínimo de 2% e altura antes da descarga, nunca ligado a engelo sem alho.
 - Duto de insulflex no comprimento de 400 mm — nunca abreviar montado.
 - Isolamento contínuo na travessa de parede, com bacia de passagem, caso de isolamento na parede condensa dentro do momento.

PROJETO PORTO REAL

RESIDENCIA UNIFAMILIAR (MANSÃO - AM) (SOLUÇÕES - PM)

PROJETO ARQUITETÔNICO

CLIMATIZAÇÃO — LINHAS FRIGORÍGENAS, DUTOS E DRENOS

BASE GEOMÉTRICA	ESCALA	EXAUSTÃO	PROVA
Linha Consolidada	1:100	ESTUDO PRELIMINAR R36	28
PROJETO (projetado)	FORMATO A1	NOVO LIBERADO PARA OBRAS	SEM ART / INT
UNIDADE MÉTRICA: mm	MILHAR 600/600/600		DE 25 REVIEWS